




melnica
_design

Дизайн - проект жилого помещения
«Дом из бруса»

email: melnica1ds@gmail.com

phone: +7 999 466 1896

instagram: [@melnica_design](https://www.instagram.com/melnica_design)

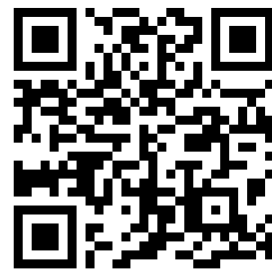

Содержание проекта


Наименование	лист
Содержание дизайн - проекта	2
План обмерный	3
План демонтажа	-
План монтажа	-
План после реконструкции	-
План расстановки мебели	4
План сантехнического оборудования	5
План напольных покрытий	6
План электрических теплых полов	-
План размещения кондиционеров	7
План потолков	8
План потолков. Разрезы	9
План светильников	10
План подключения светильников	11
План расстановки розеток	12
План проемов и дверей	13
План разверток стен	14
Развертка стен	15-19
Визуализации	20-50



melnica
_design

email: melnica1ds@gmail.com
phone: +7 999 466 1896
instagram: @melnica_design


	ФИО	подпись	дата	Содержание дизайн - проекта		
Выполнил				Жилой дом из бруса		
Согласовал					лист - 02	этаж 1

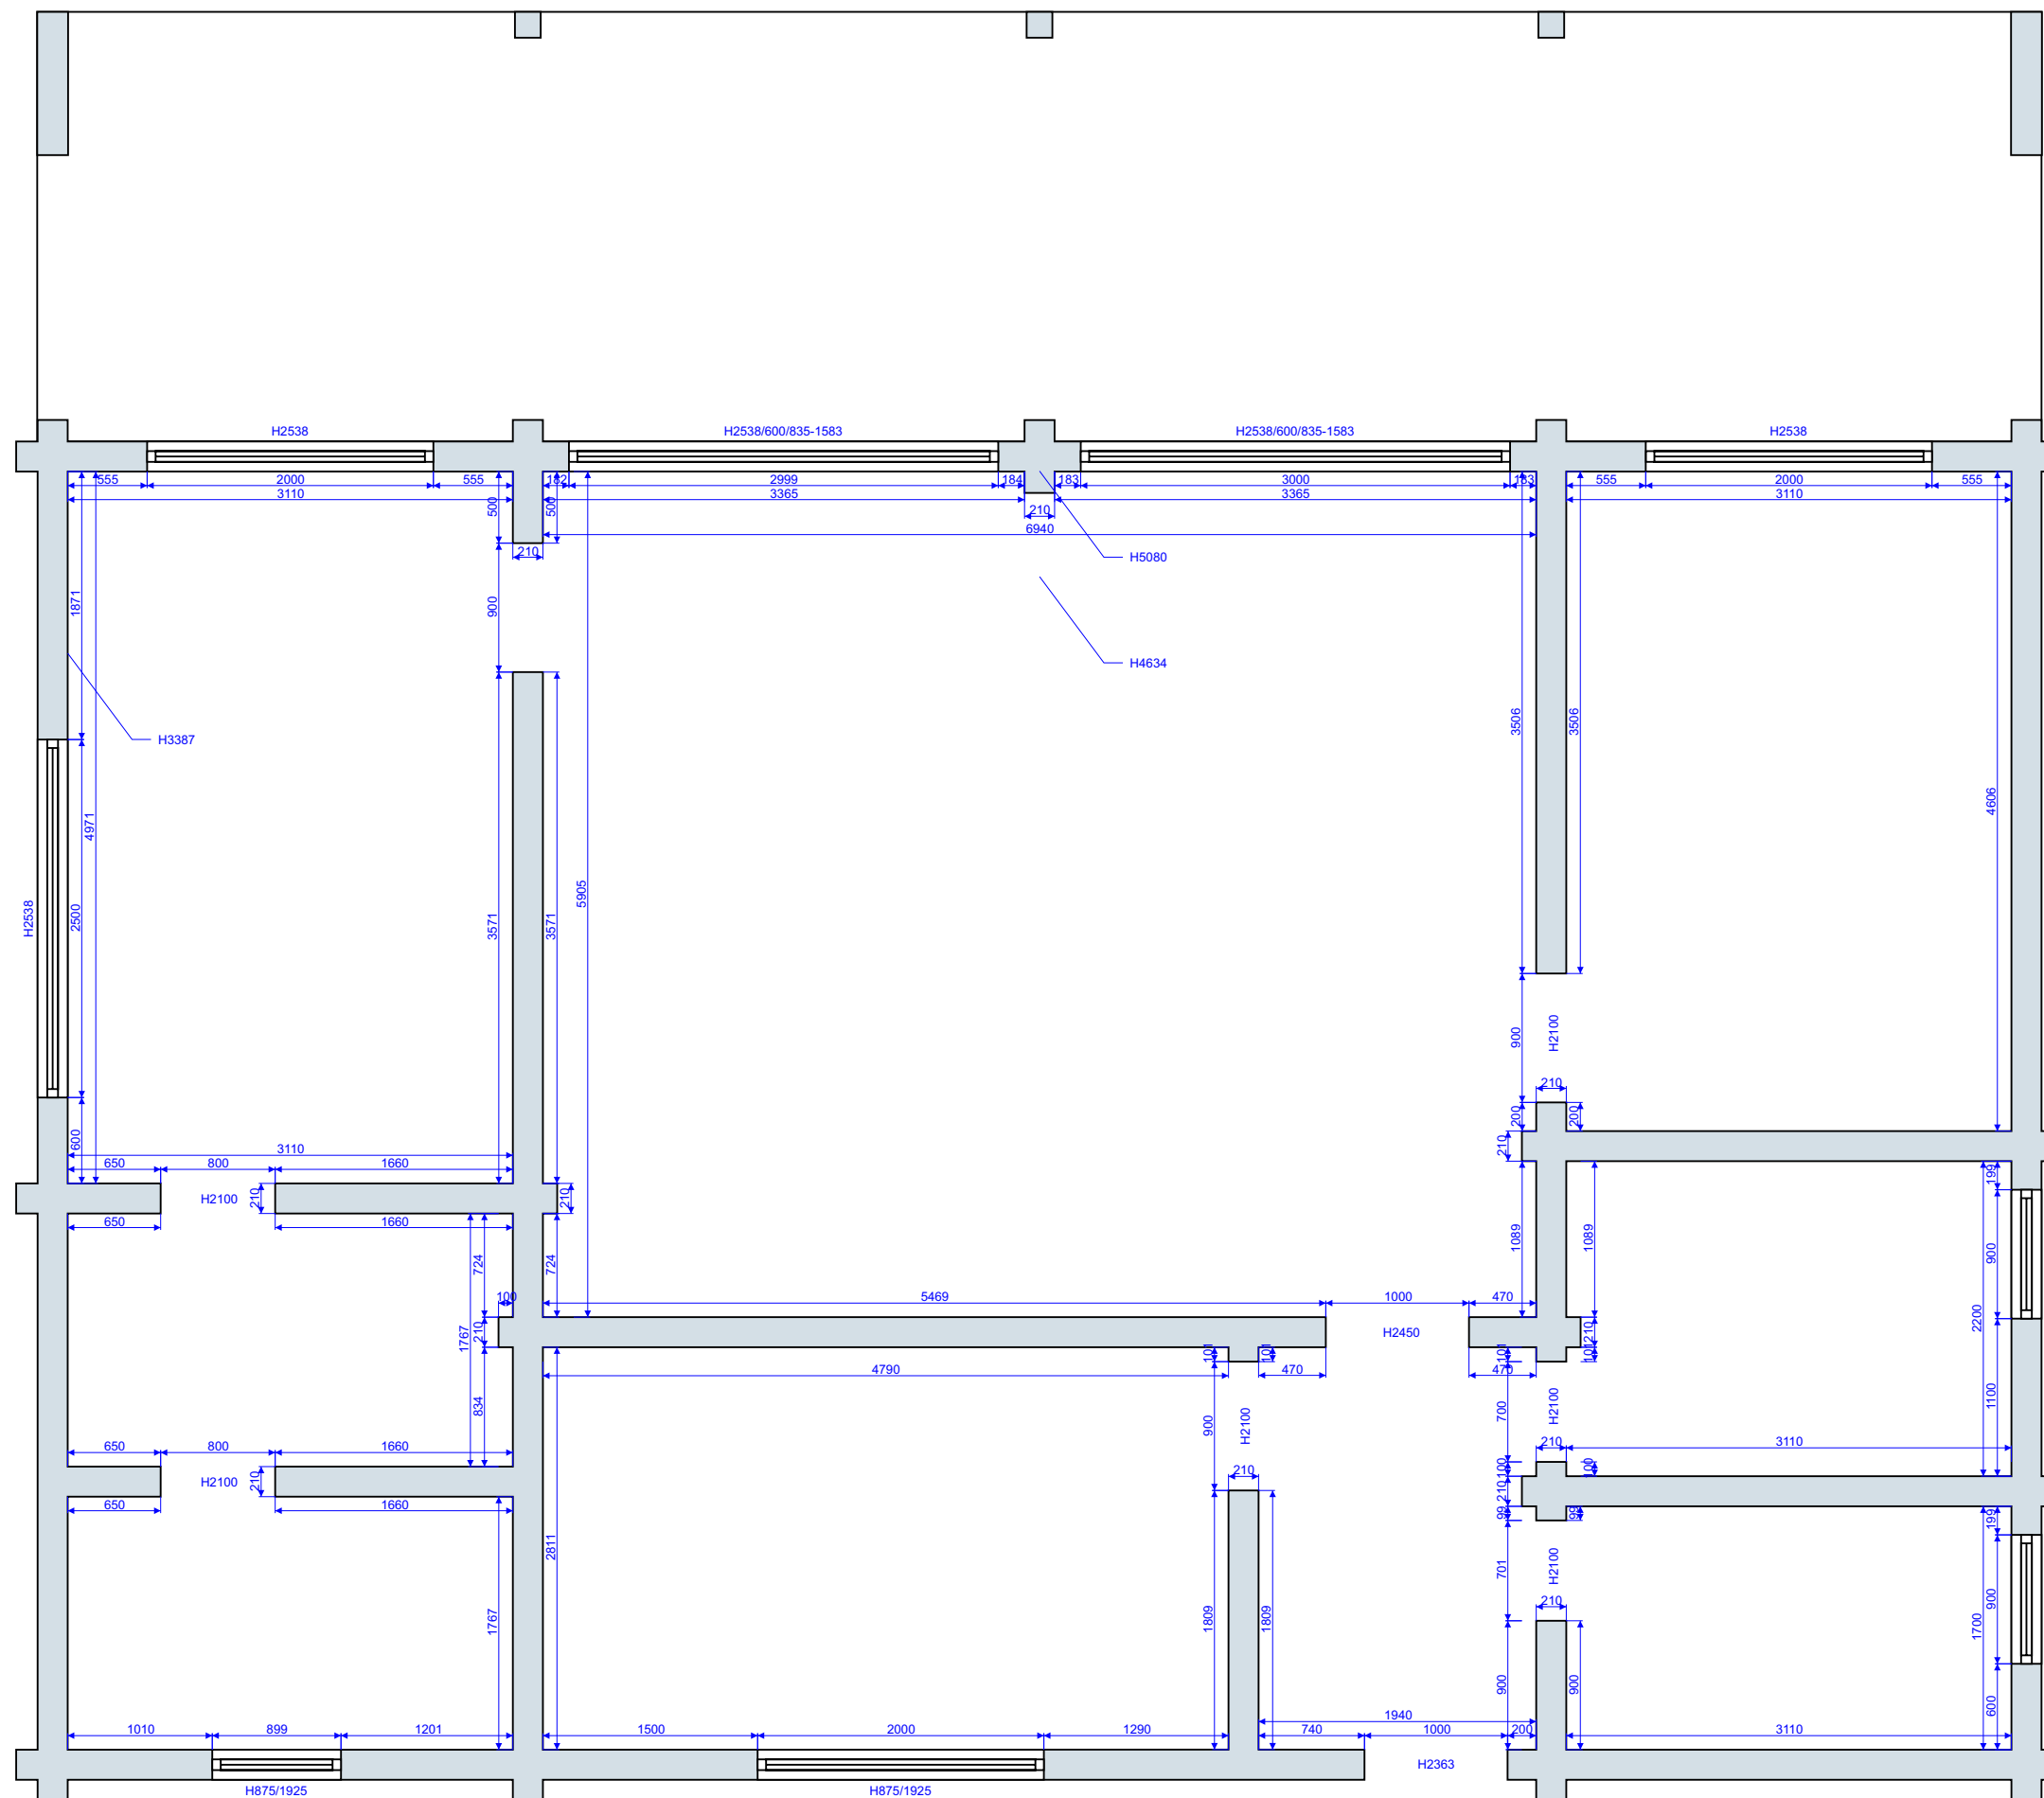

**melnica
_design**

email: melnica1ds@gmail.com
phone: +7 999 466 1896
instagram: @melnica_design


	ФИО	подпись	дата	План обмерный		
Выполнил				Жилой дом из бруса		
Согласовал				масштаб 1:50	лист - 03	этаж 1

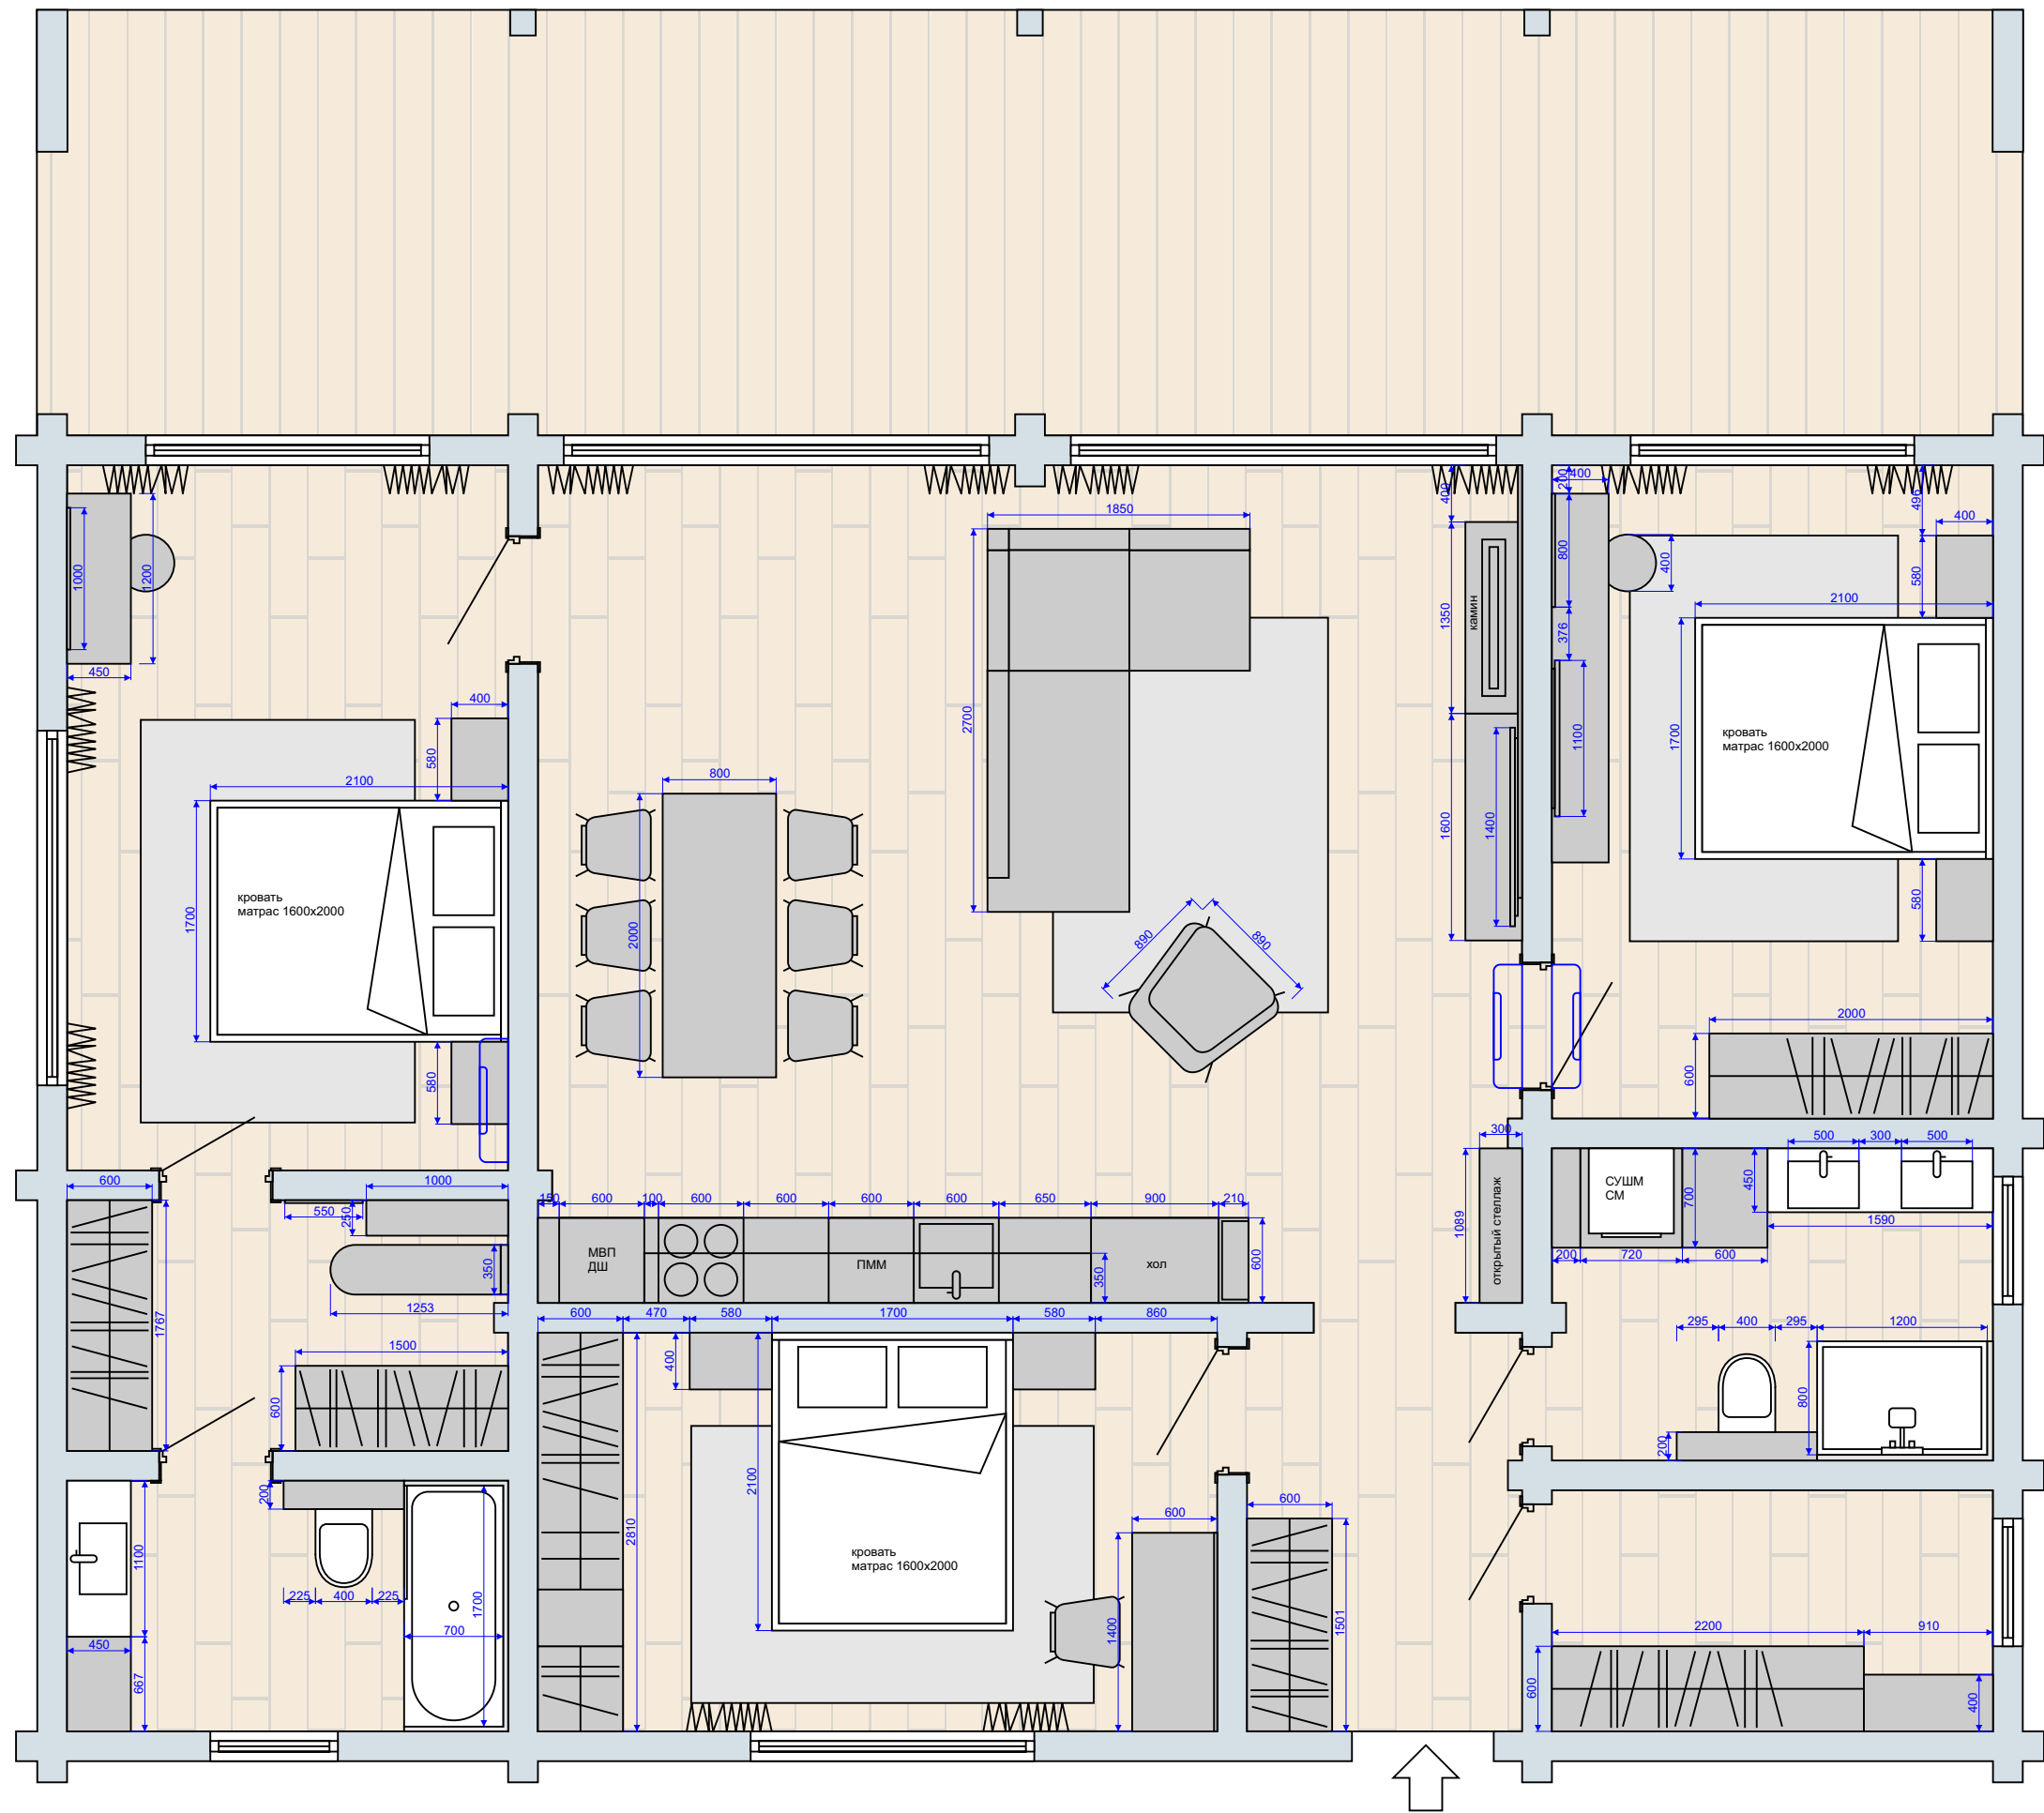

**melnica
_design**

email: melnica1ds@gmail.com
phone: +7 999 466 1896
instagram: @melnica_design


	ФИО	подпись	дата	План расстановки мебели		
Выполнил				Жилой дом из бруса		
Согласовал				масштаб 1:50	лист - 04	этаж 1

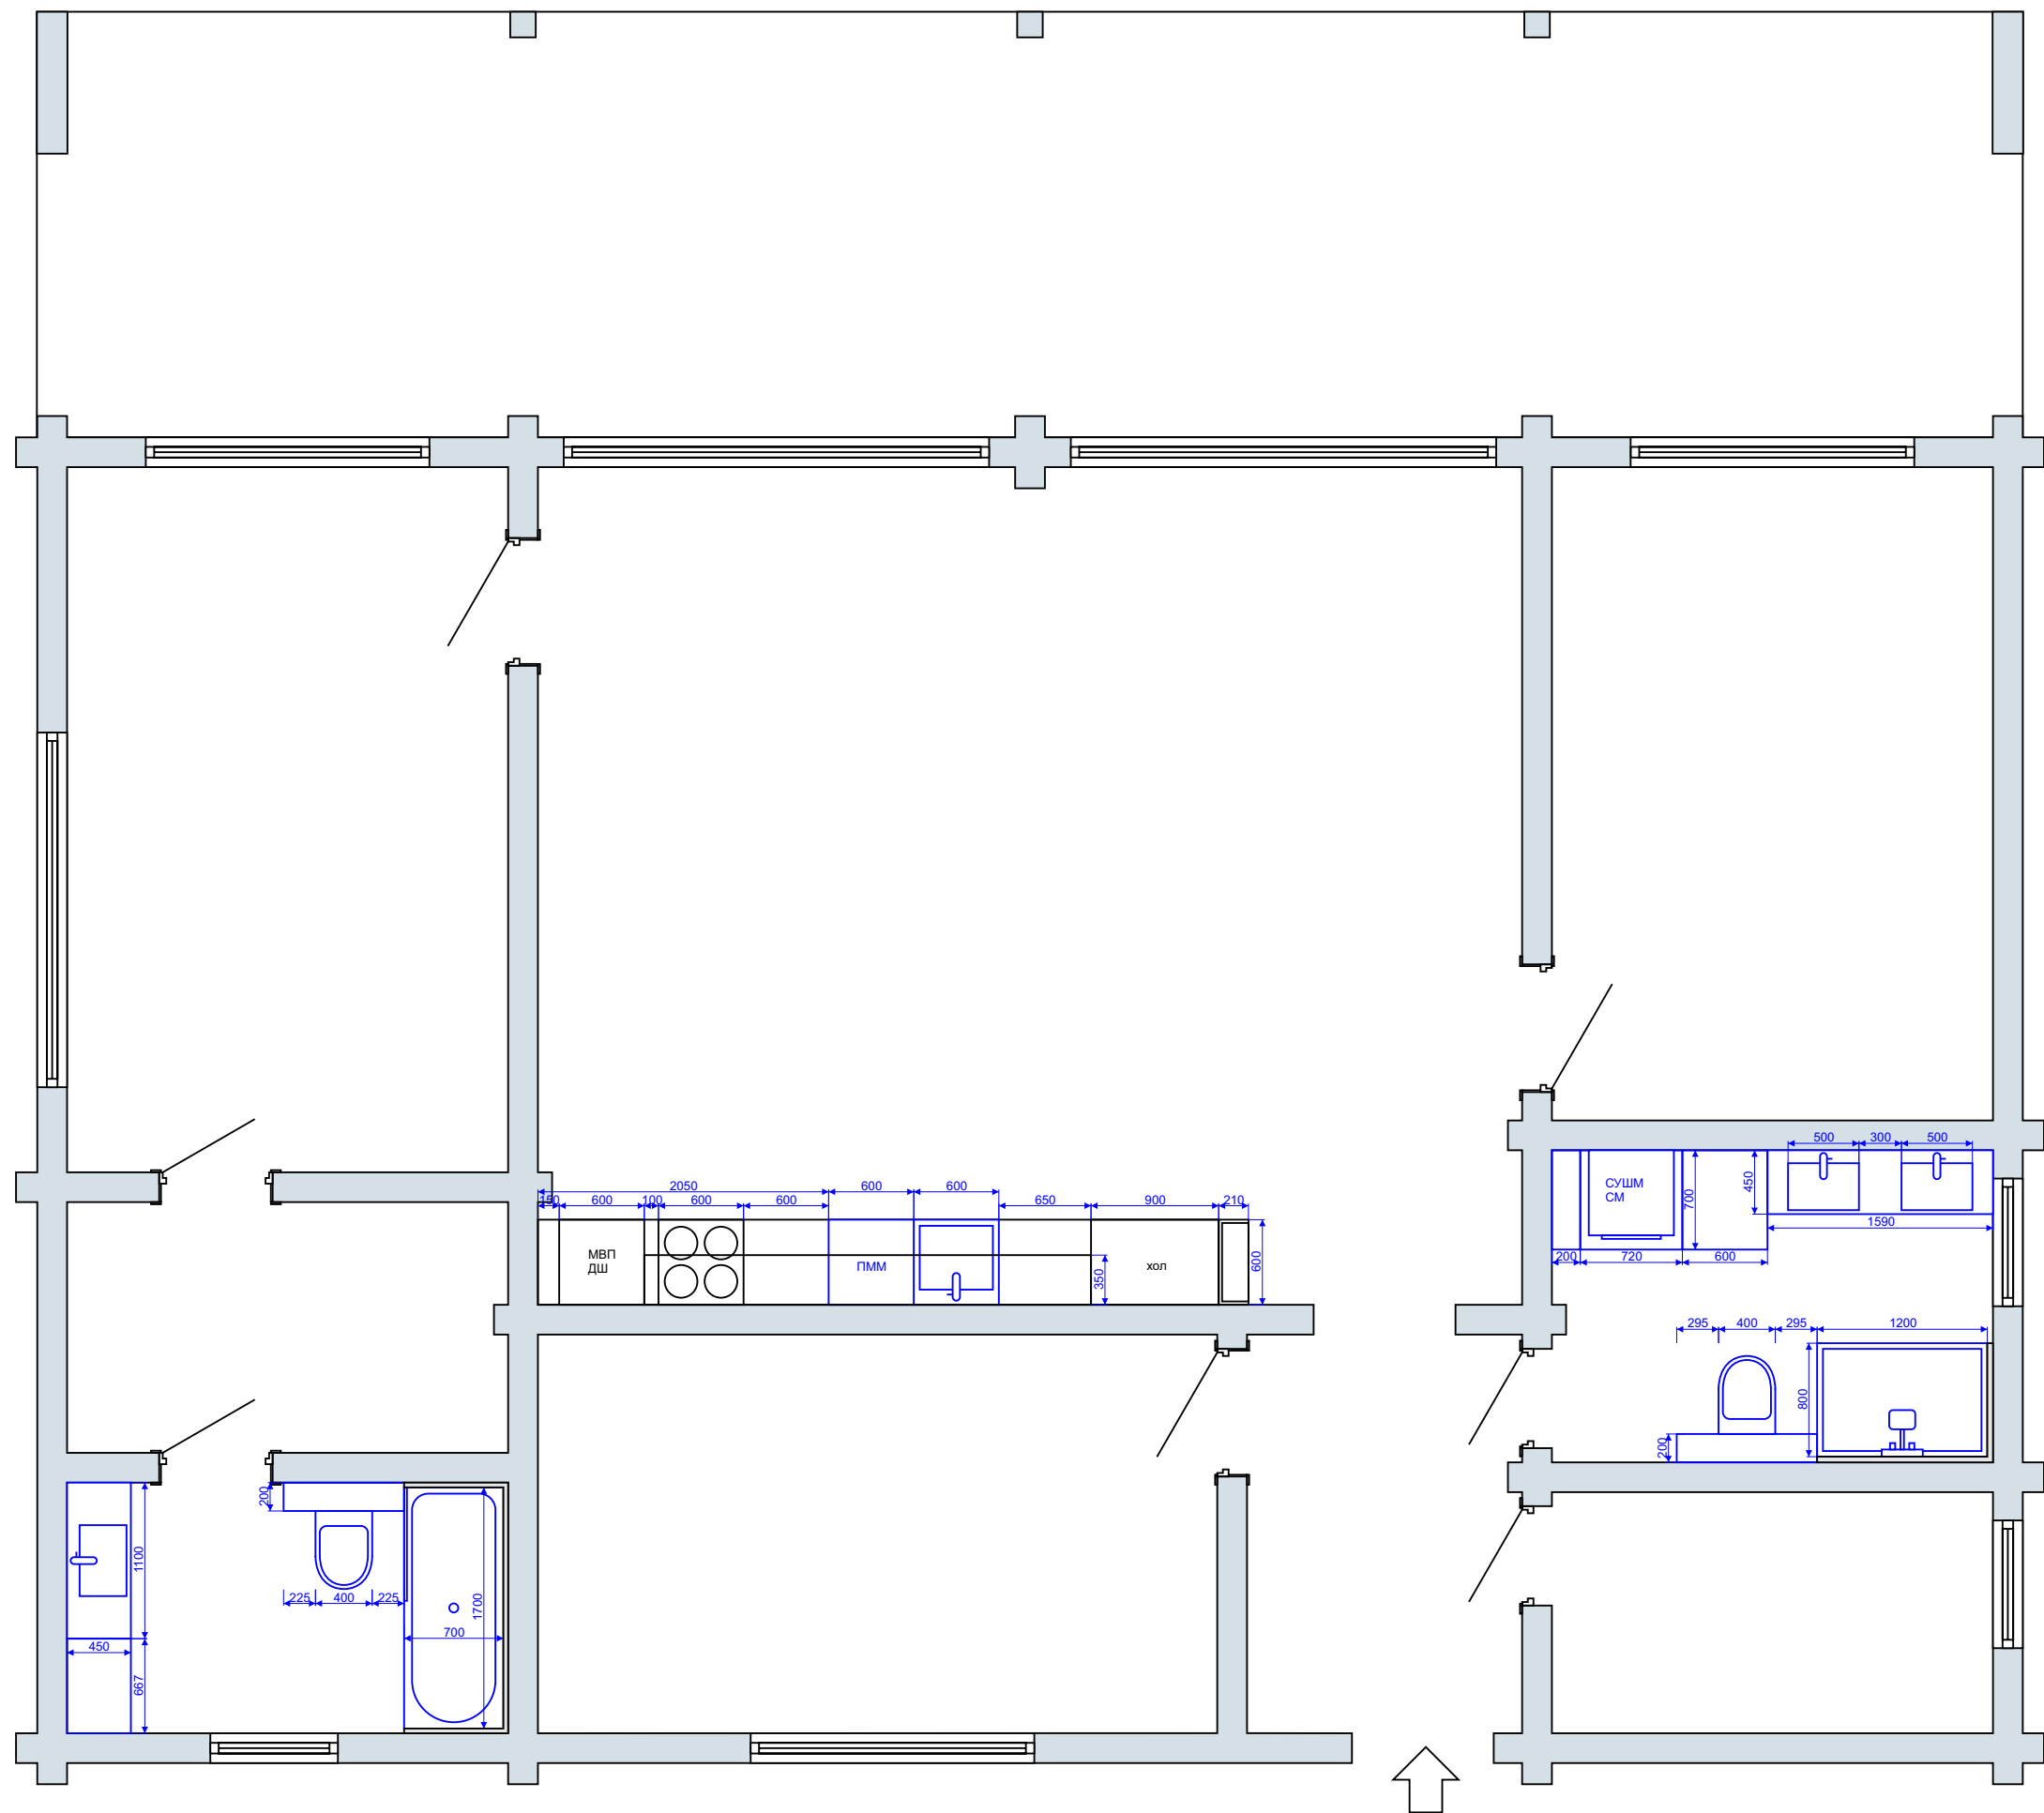

**melnica
_design**

email: melnica1ds@gmail.com
phone: +7 999 466 1896
instagram: @melnica_design


	ФИО	подпись	дата	План сантехнического оборудования		
Выполнил				Жилой дом из бруса		
Согласовал				масштаб 1:50	лист - 05	этаж 1

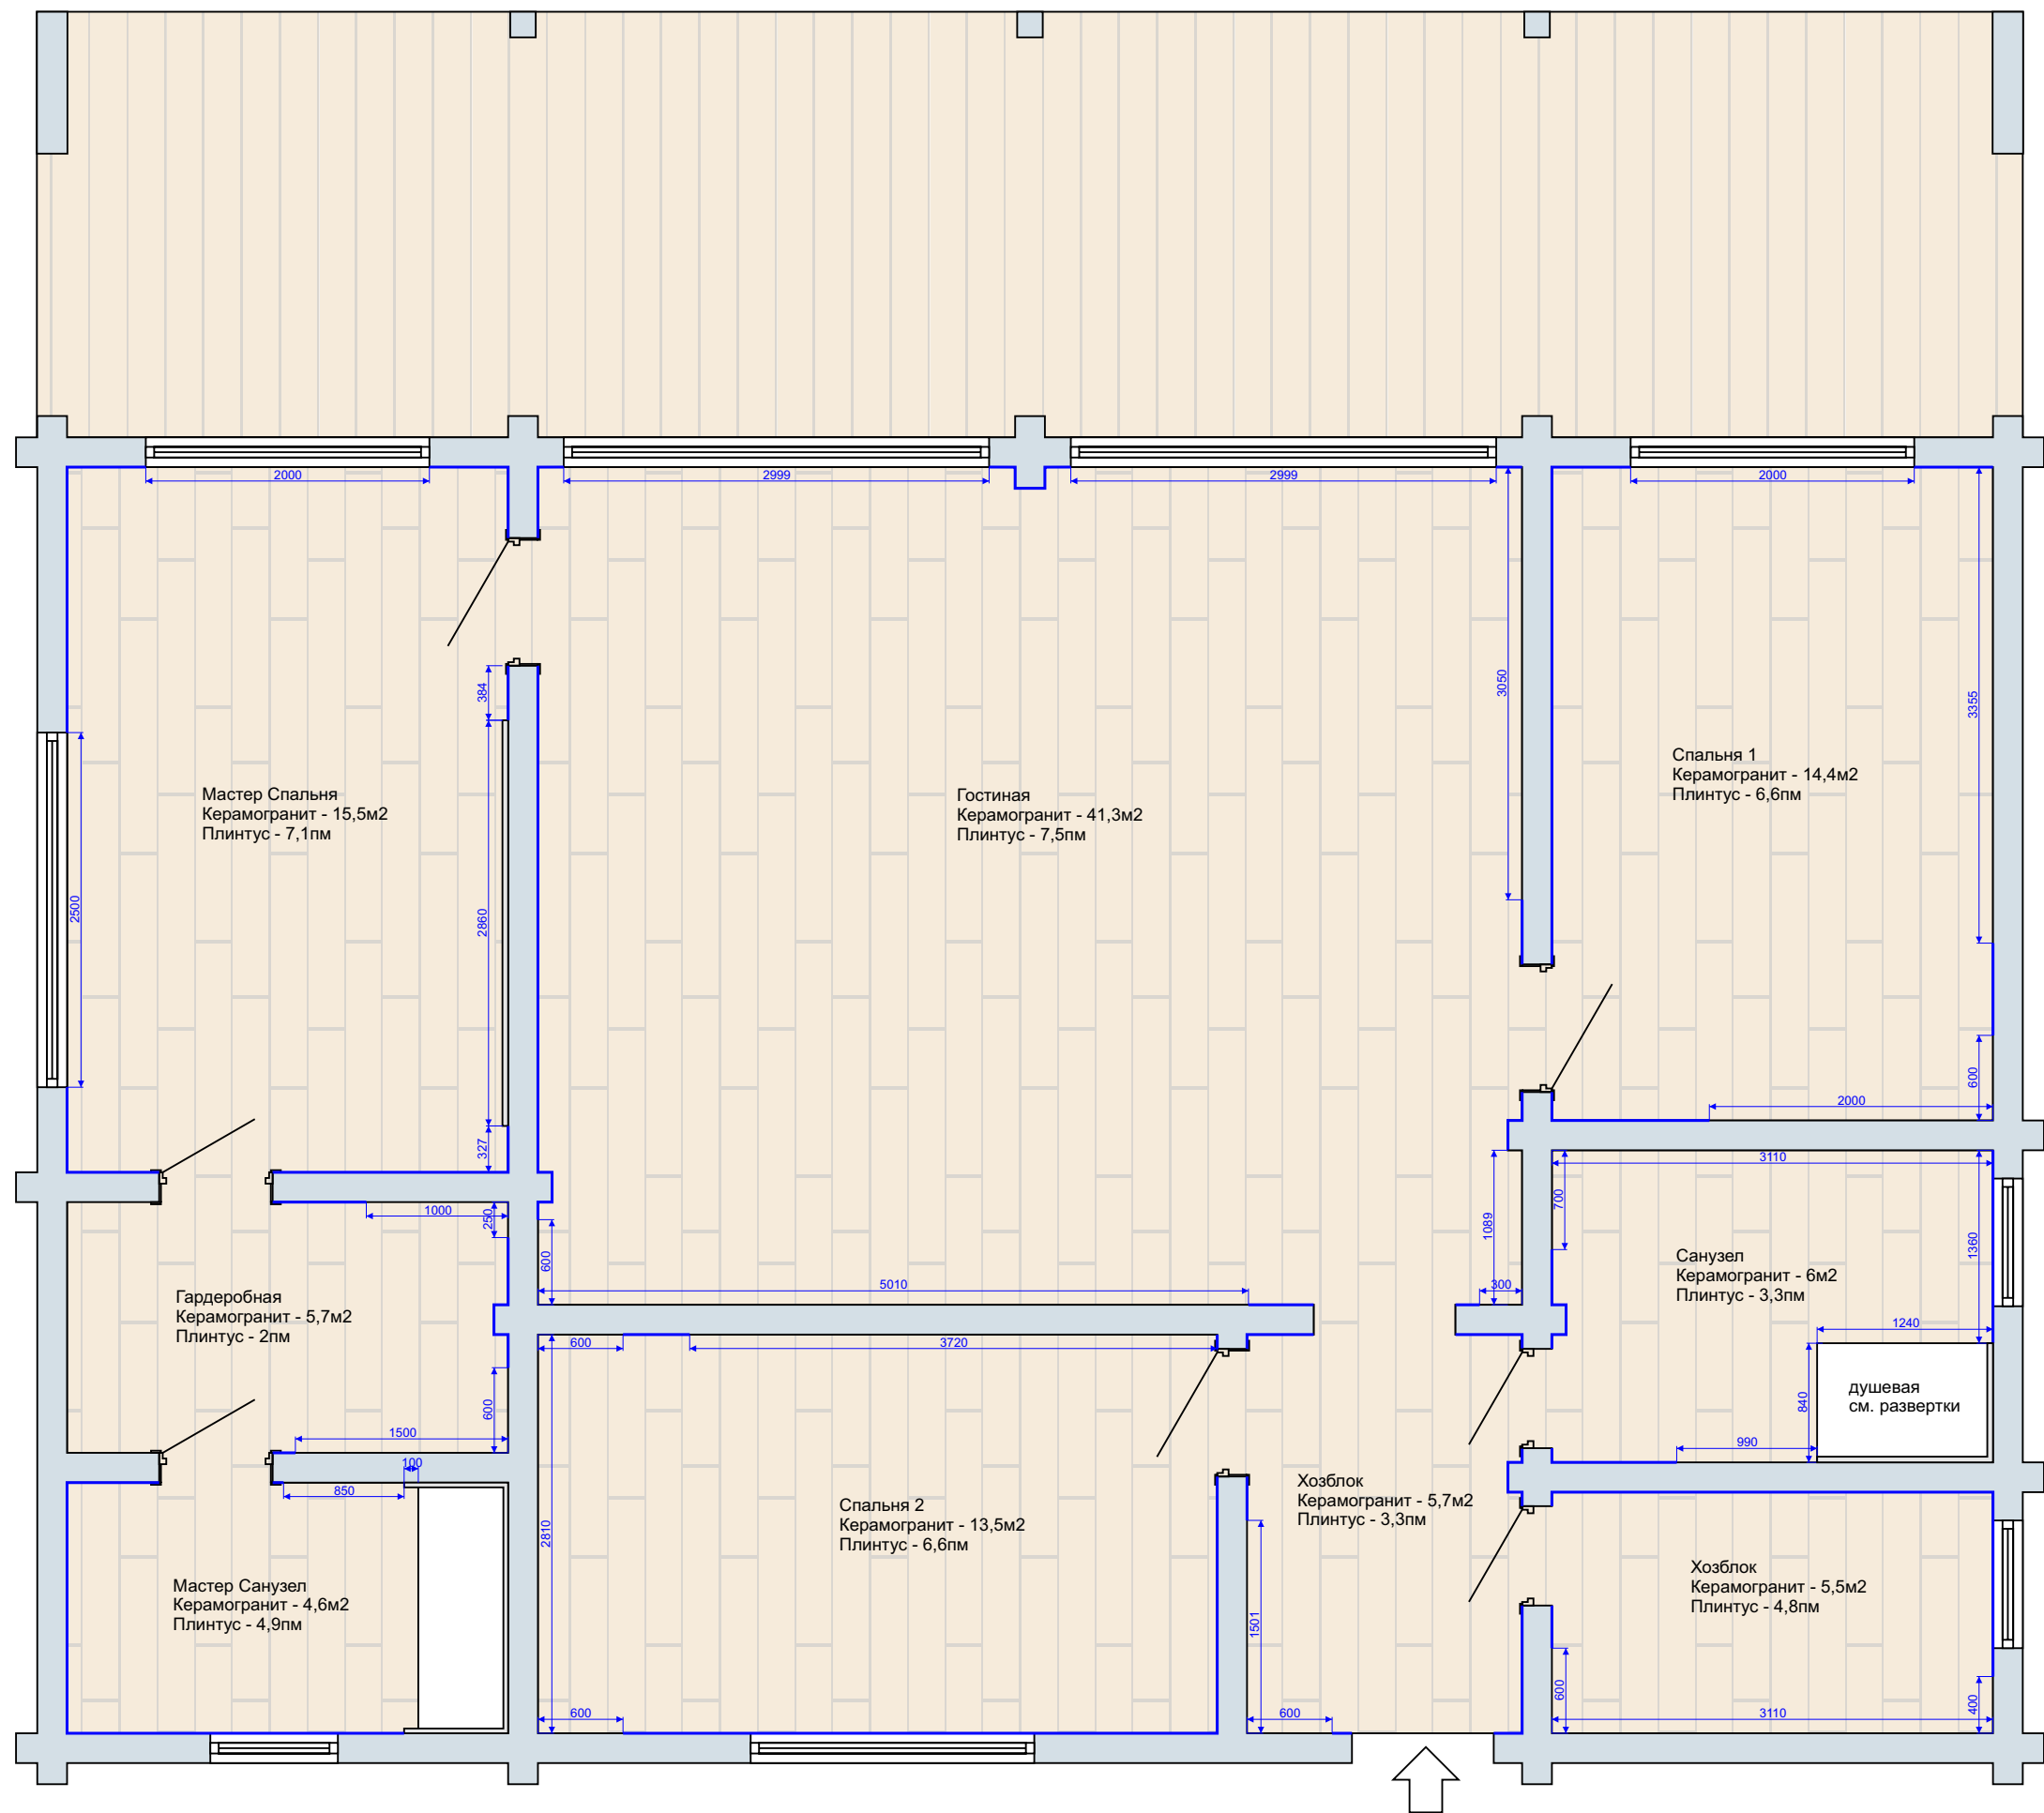

**melnica
_design**

email: melnica1ds@gmail.com
phone: +7 999 466 1896
instagram: @melnica_design


	ФИО	подпись	дата	План напольных покрытий		
Выполнил				Жилой дом из бруса		
Согласовал				масштаб 1:50	лист - 06	этаж 1

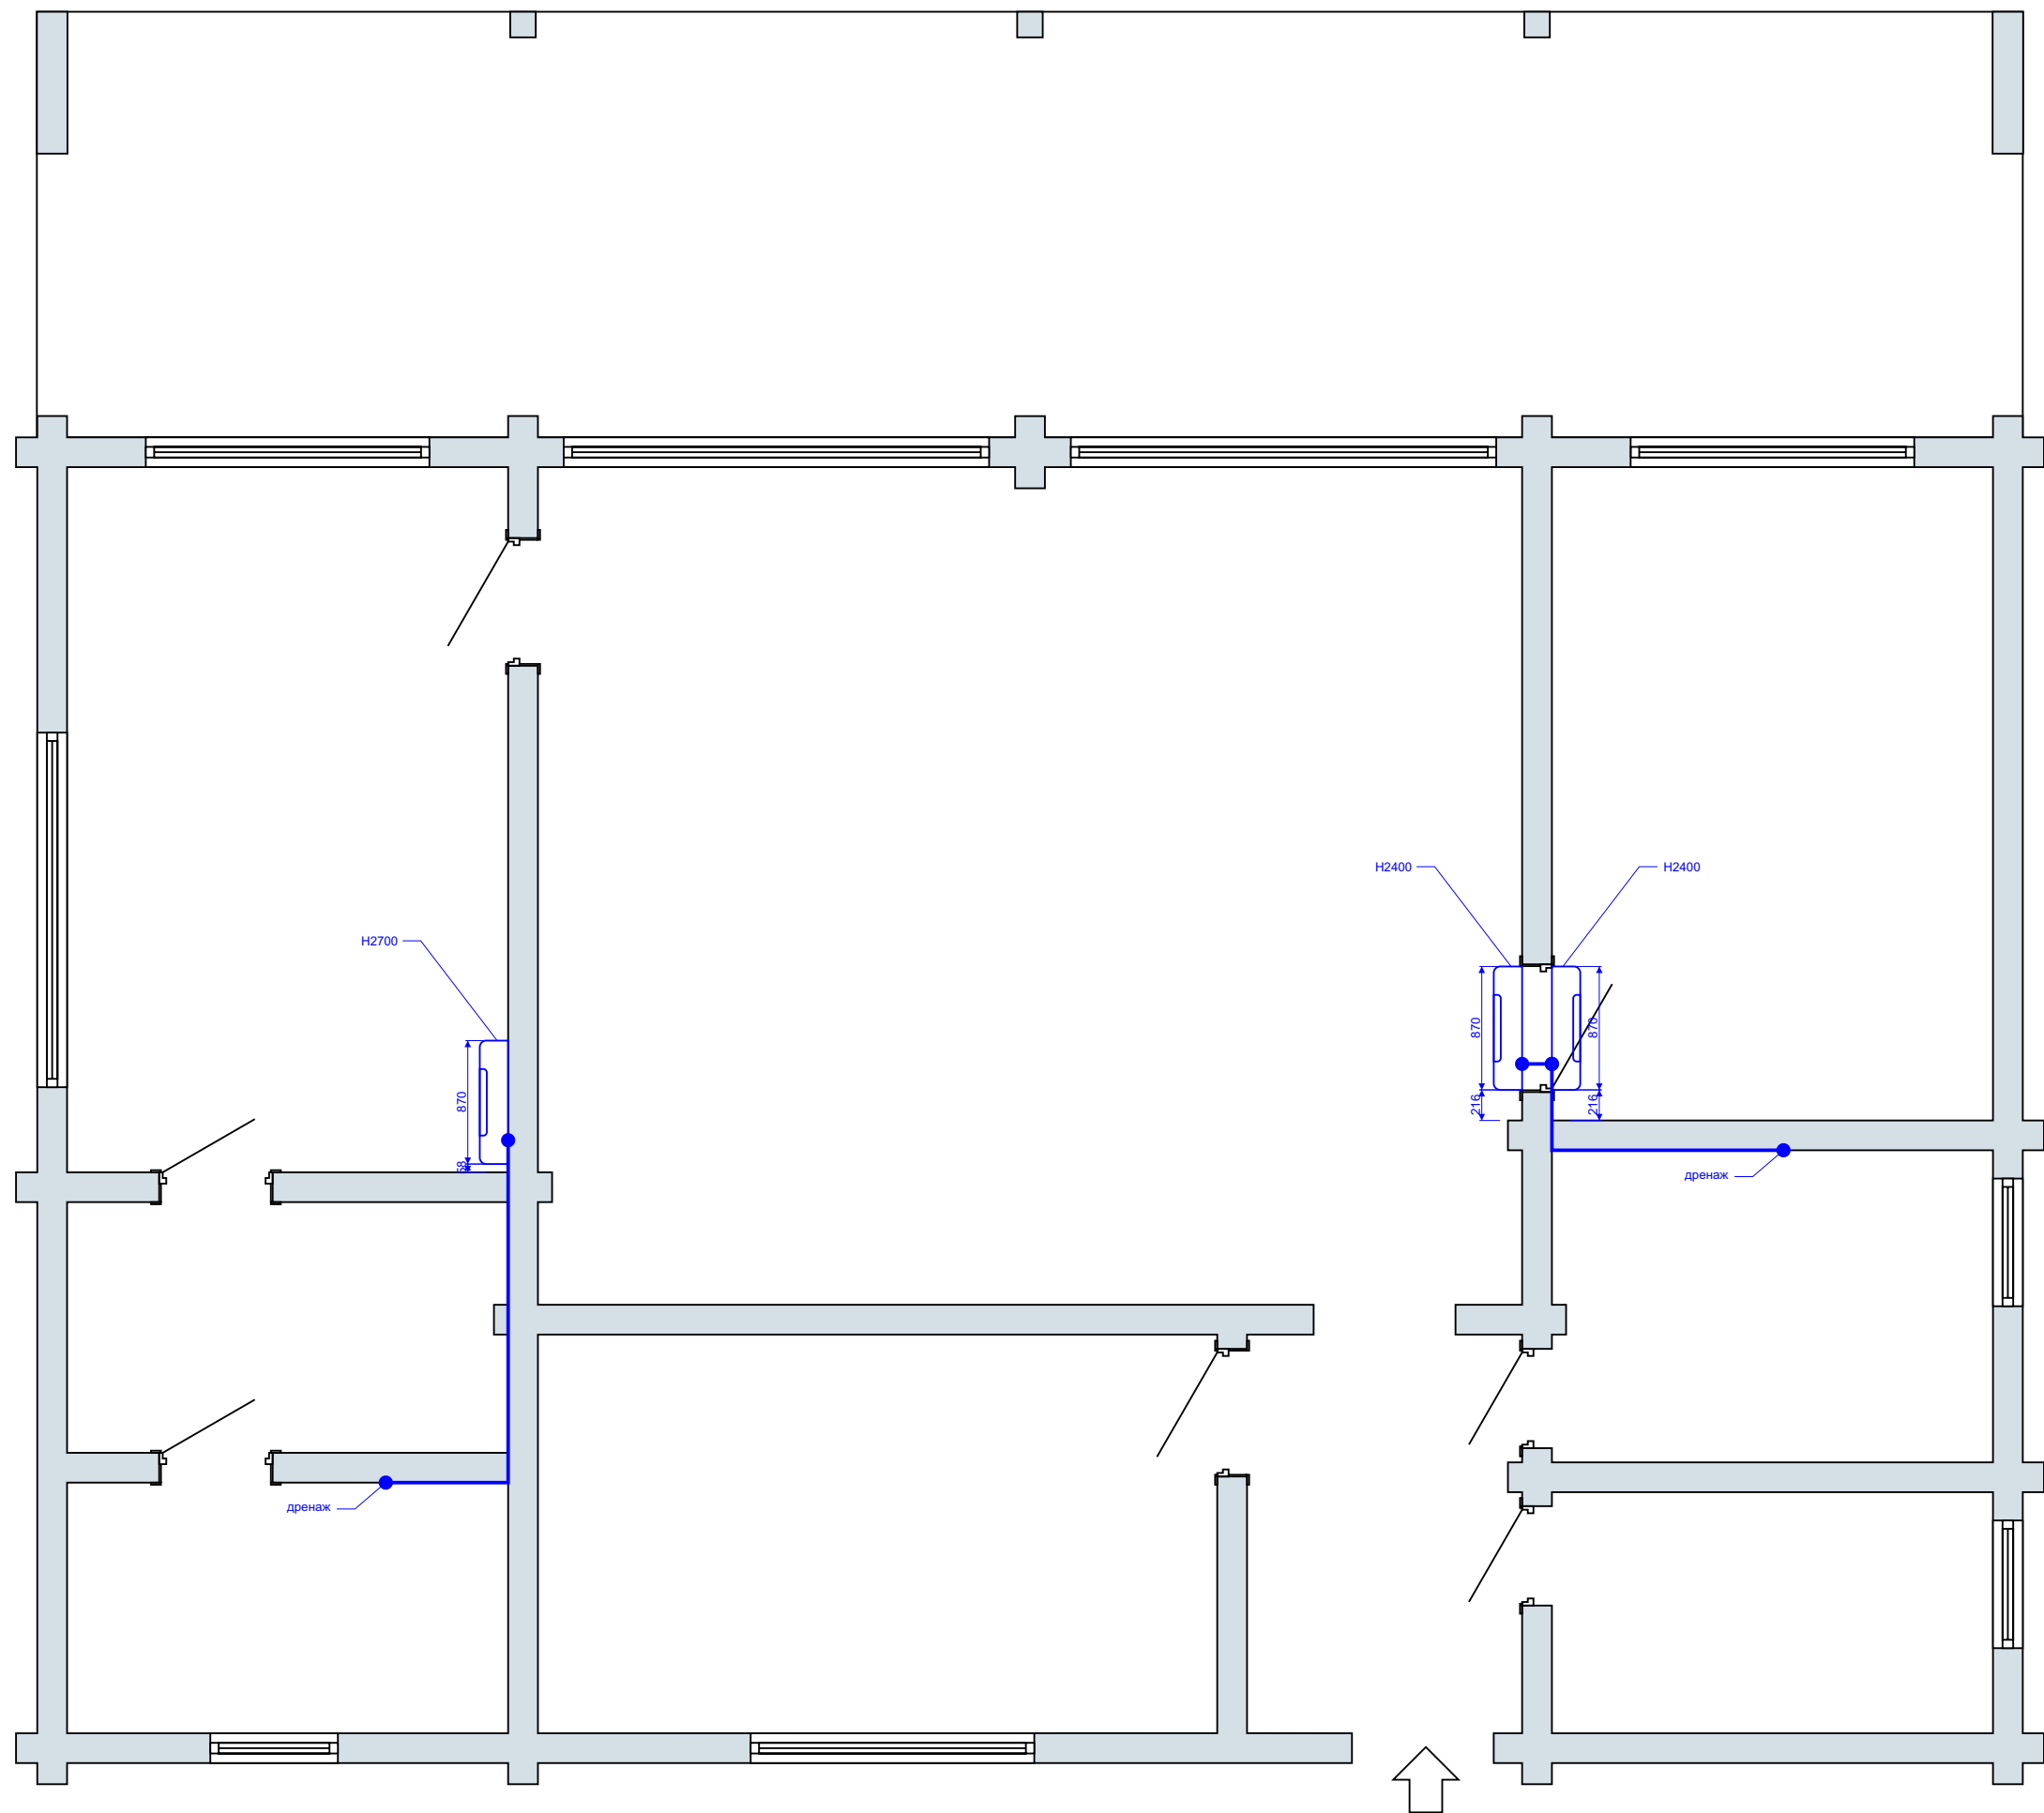

melnica
_design

email: melnica1ds@gmail.com
phone: +7 999 466 1896
instagram: @melnica_design


	ФИО	подпись	дата	План размещения кондиционеров		
Выполнил				Жилой дом из бруса		
Согласовал				масштаб 1:50	лист - 07	этаж 1

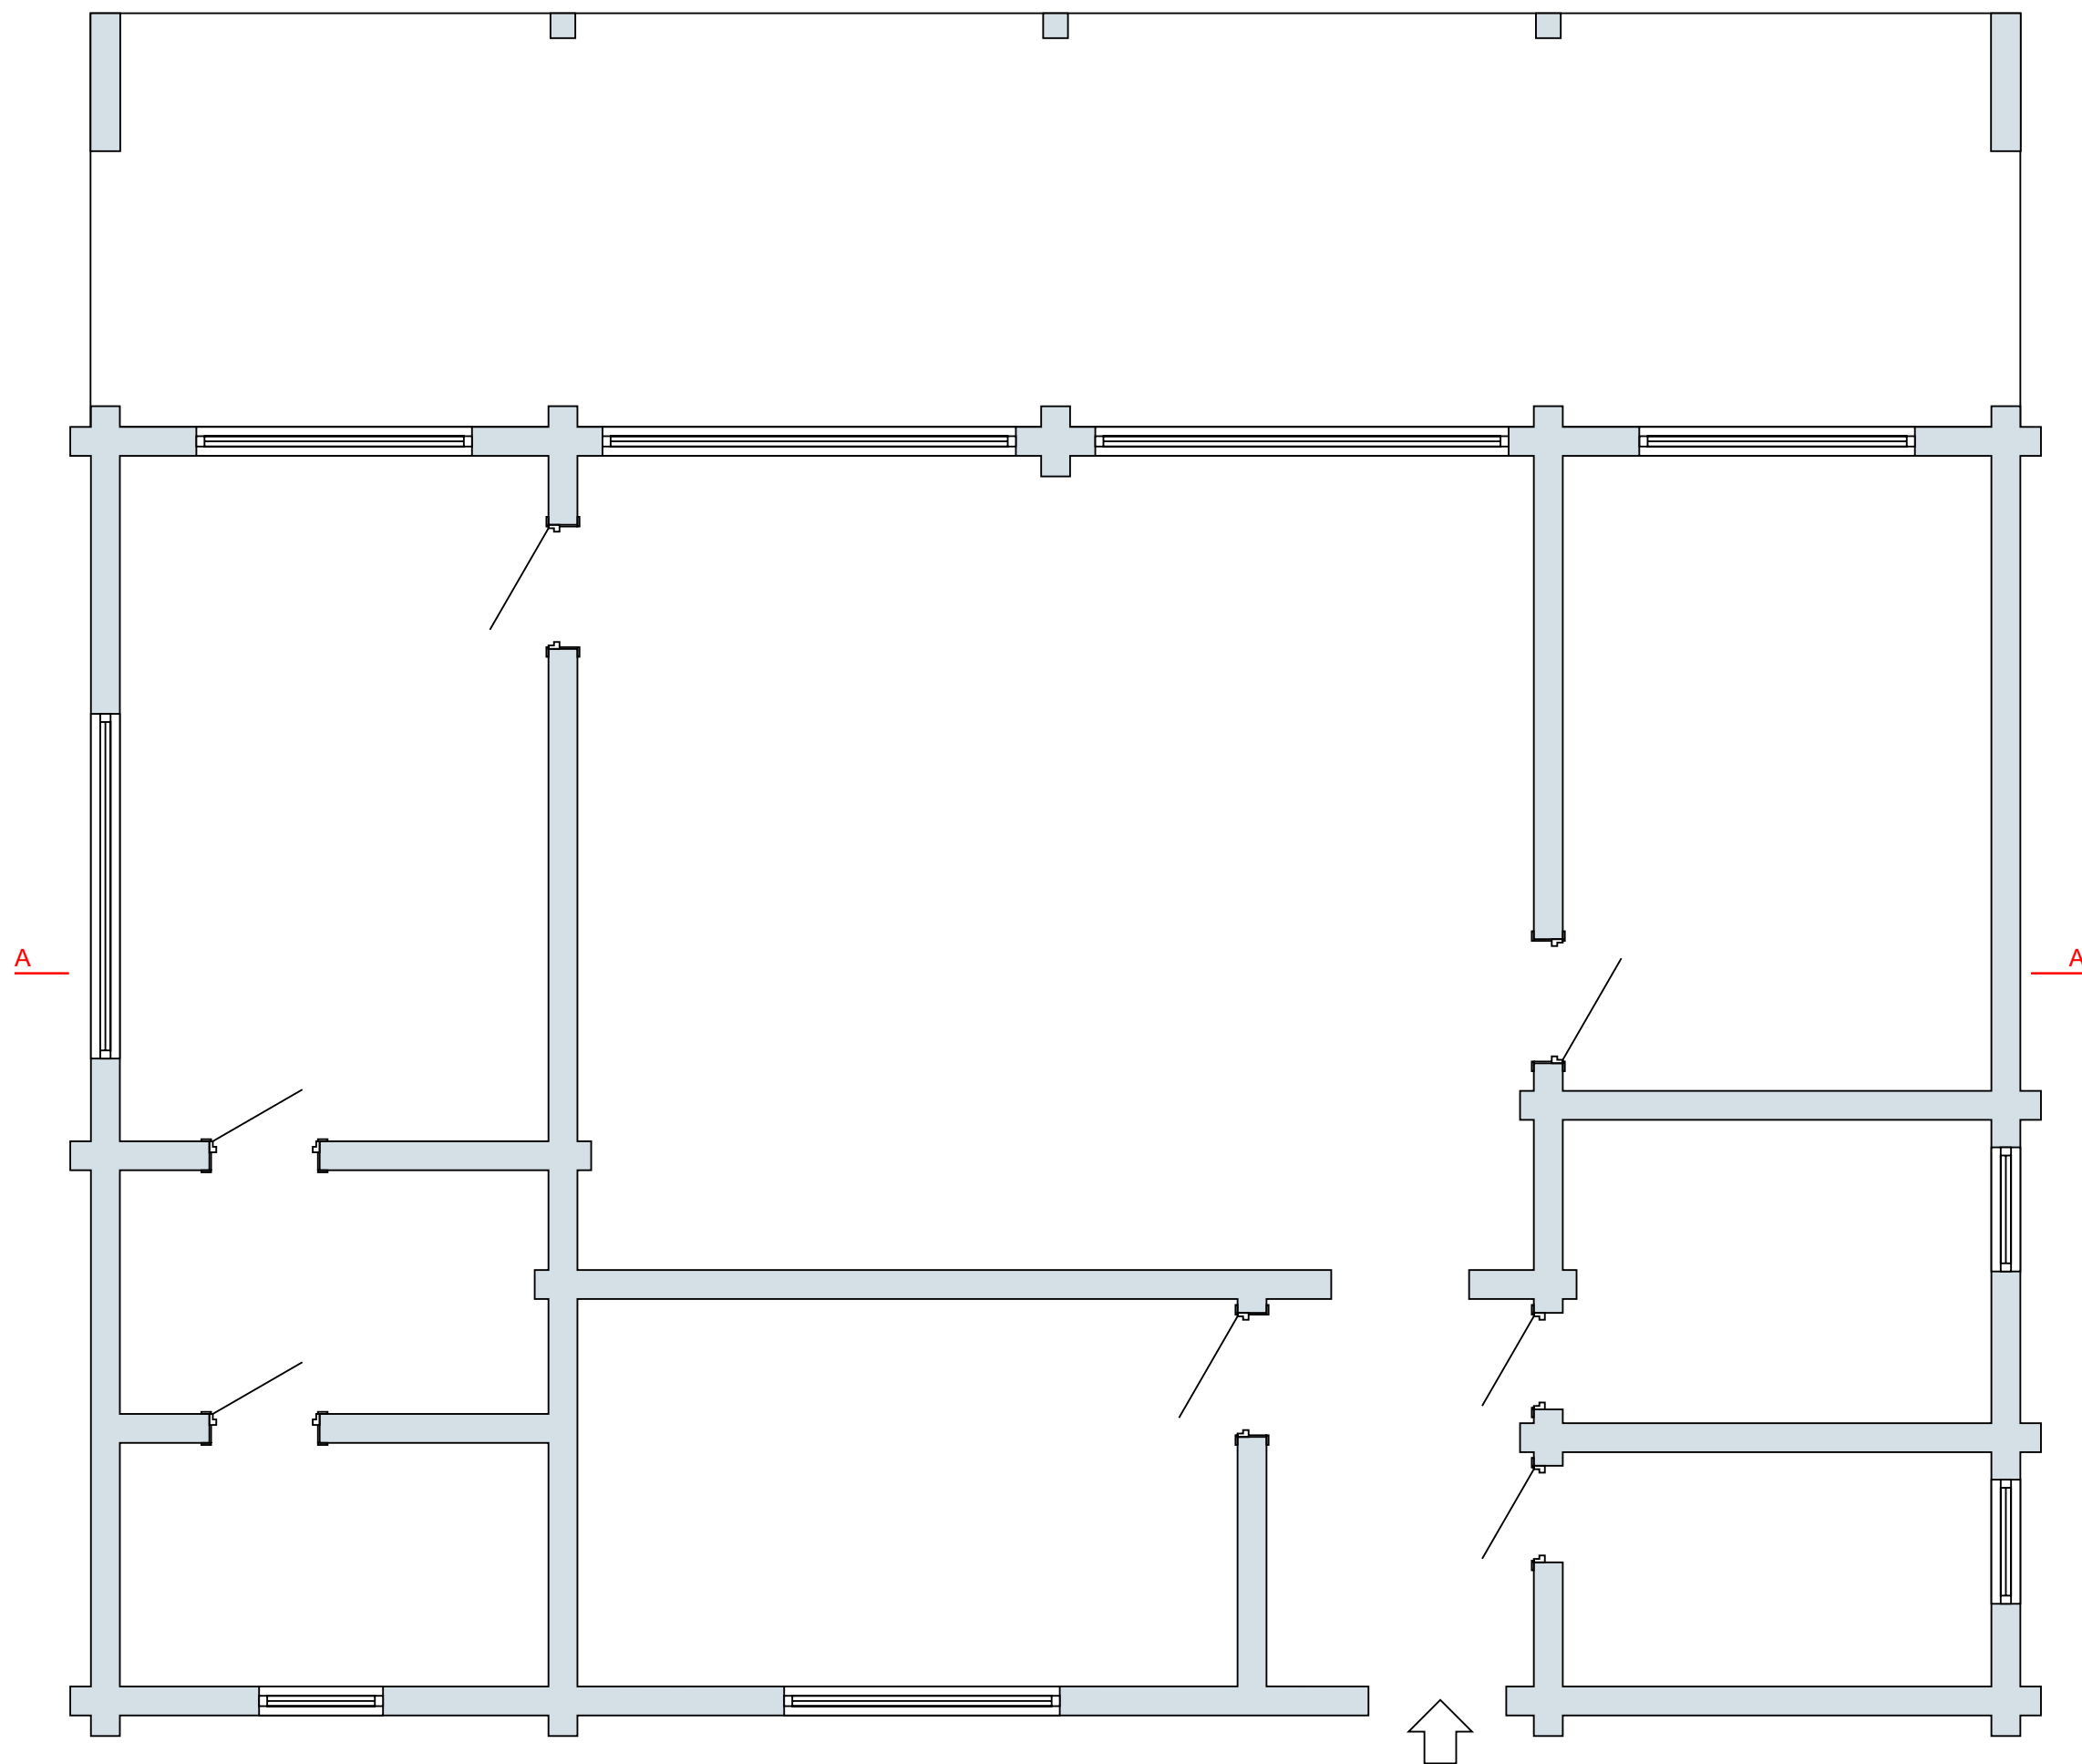

**melnica
_design**

email: melnica1ds@gmail.com
phone: +7 999 466 1896
instagram: @melnica_design


	ФИО	подпись	дата	План потолков		
Выполнил				Жилой дом из бруса		
Согласовал				масштаб 1:50	лист - 08	этаж 1

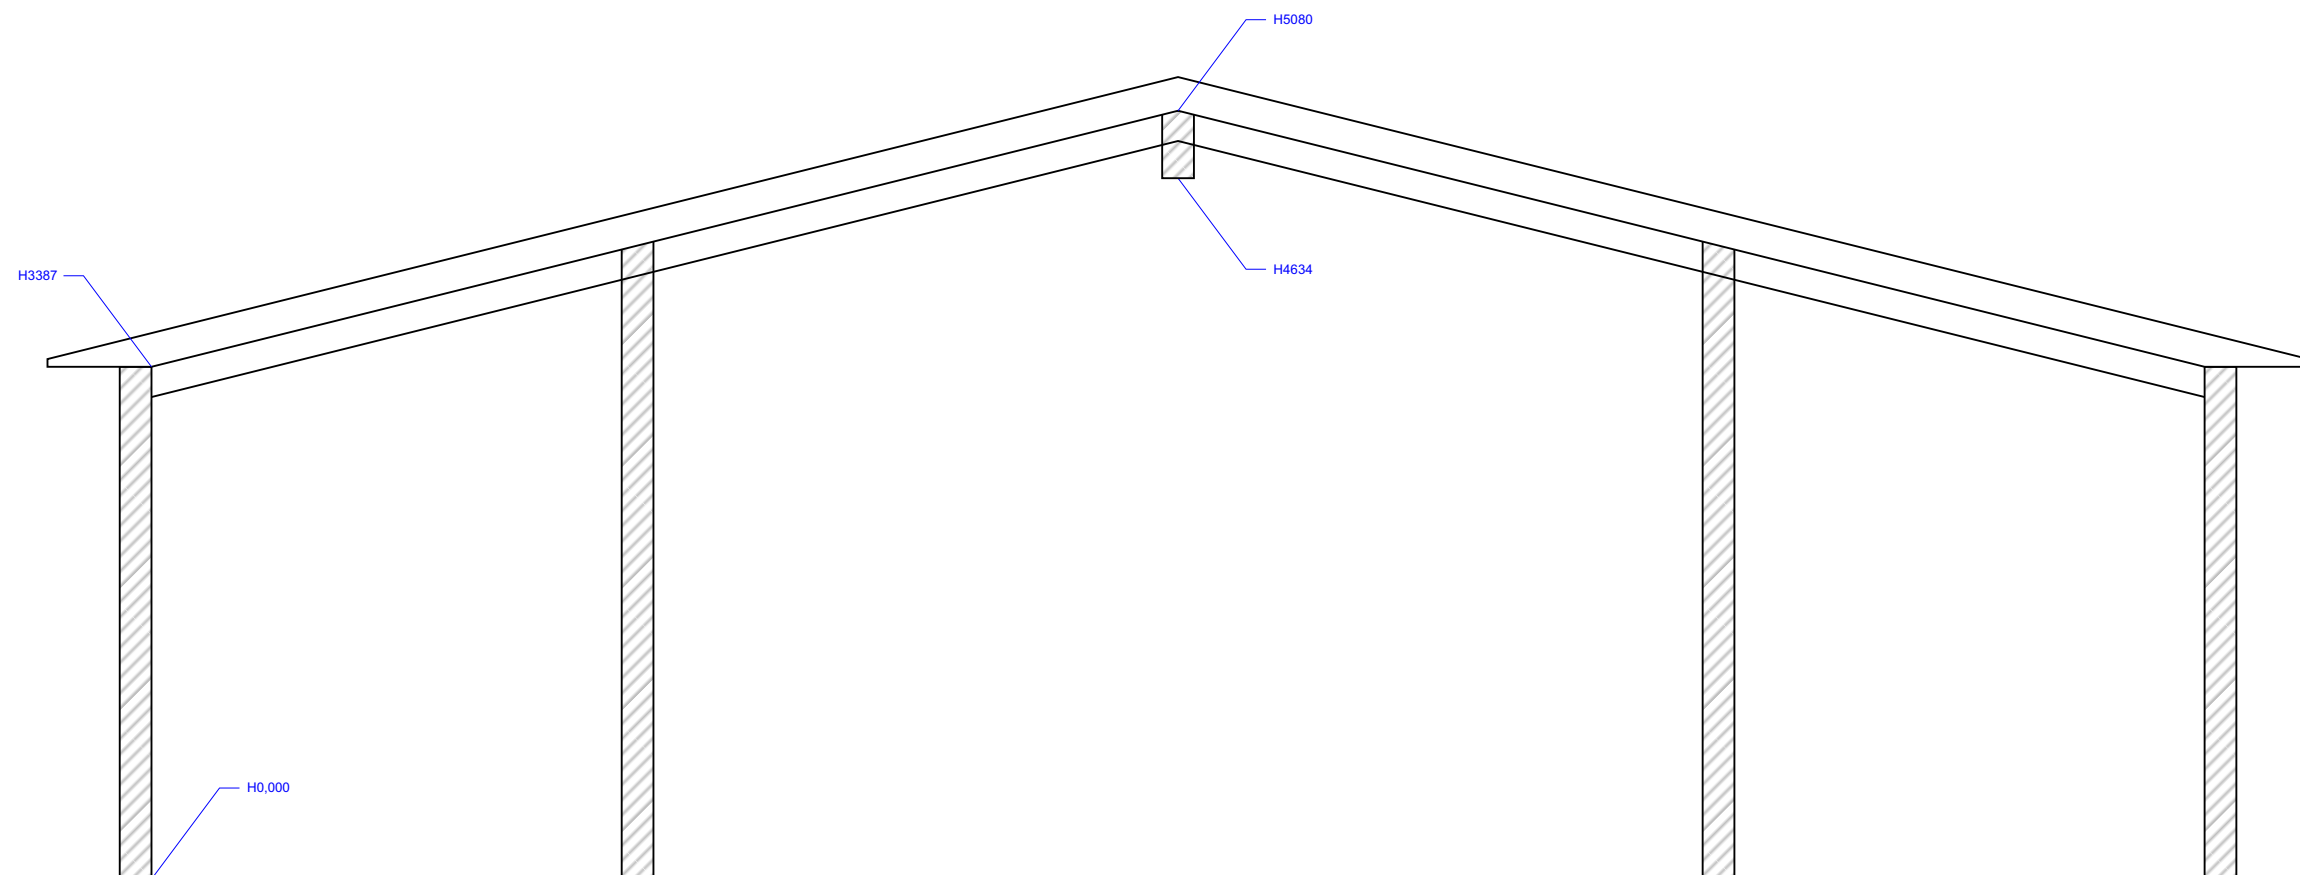

melnica
_design

email: melnica1ds@gmail.com
phone: +7 999 466 1896
instagram: @melnica_design


	ФИО	подпись	дата	План потолков. Разрезы		
Выполнил				Жилой дом из бруса		
Согласовал				масштаб 1:50	лист - 09	этаж 1

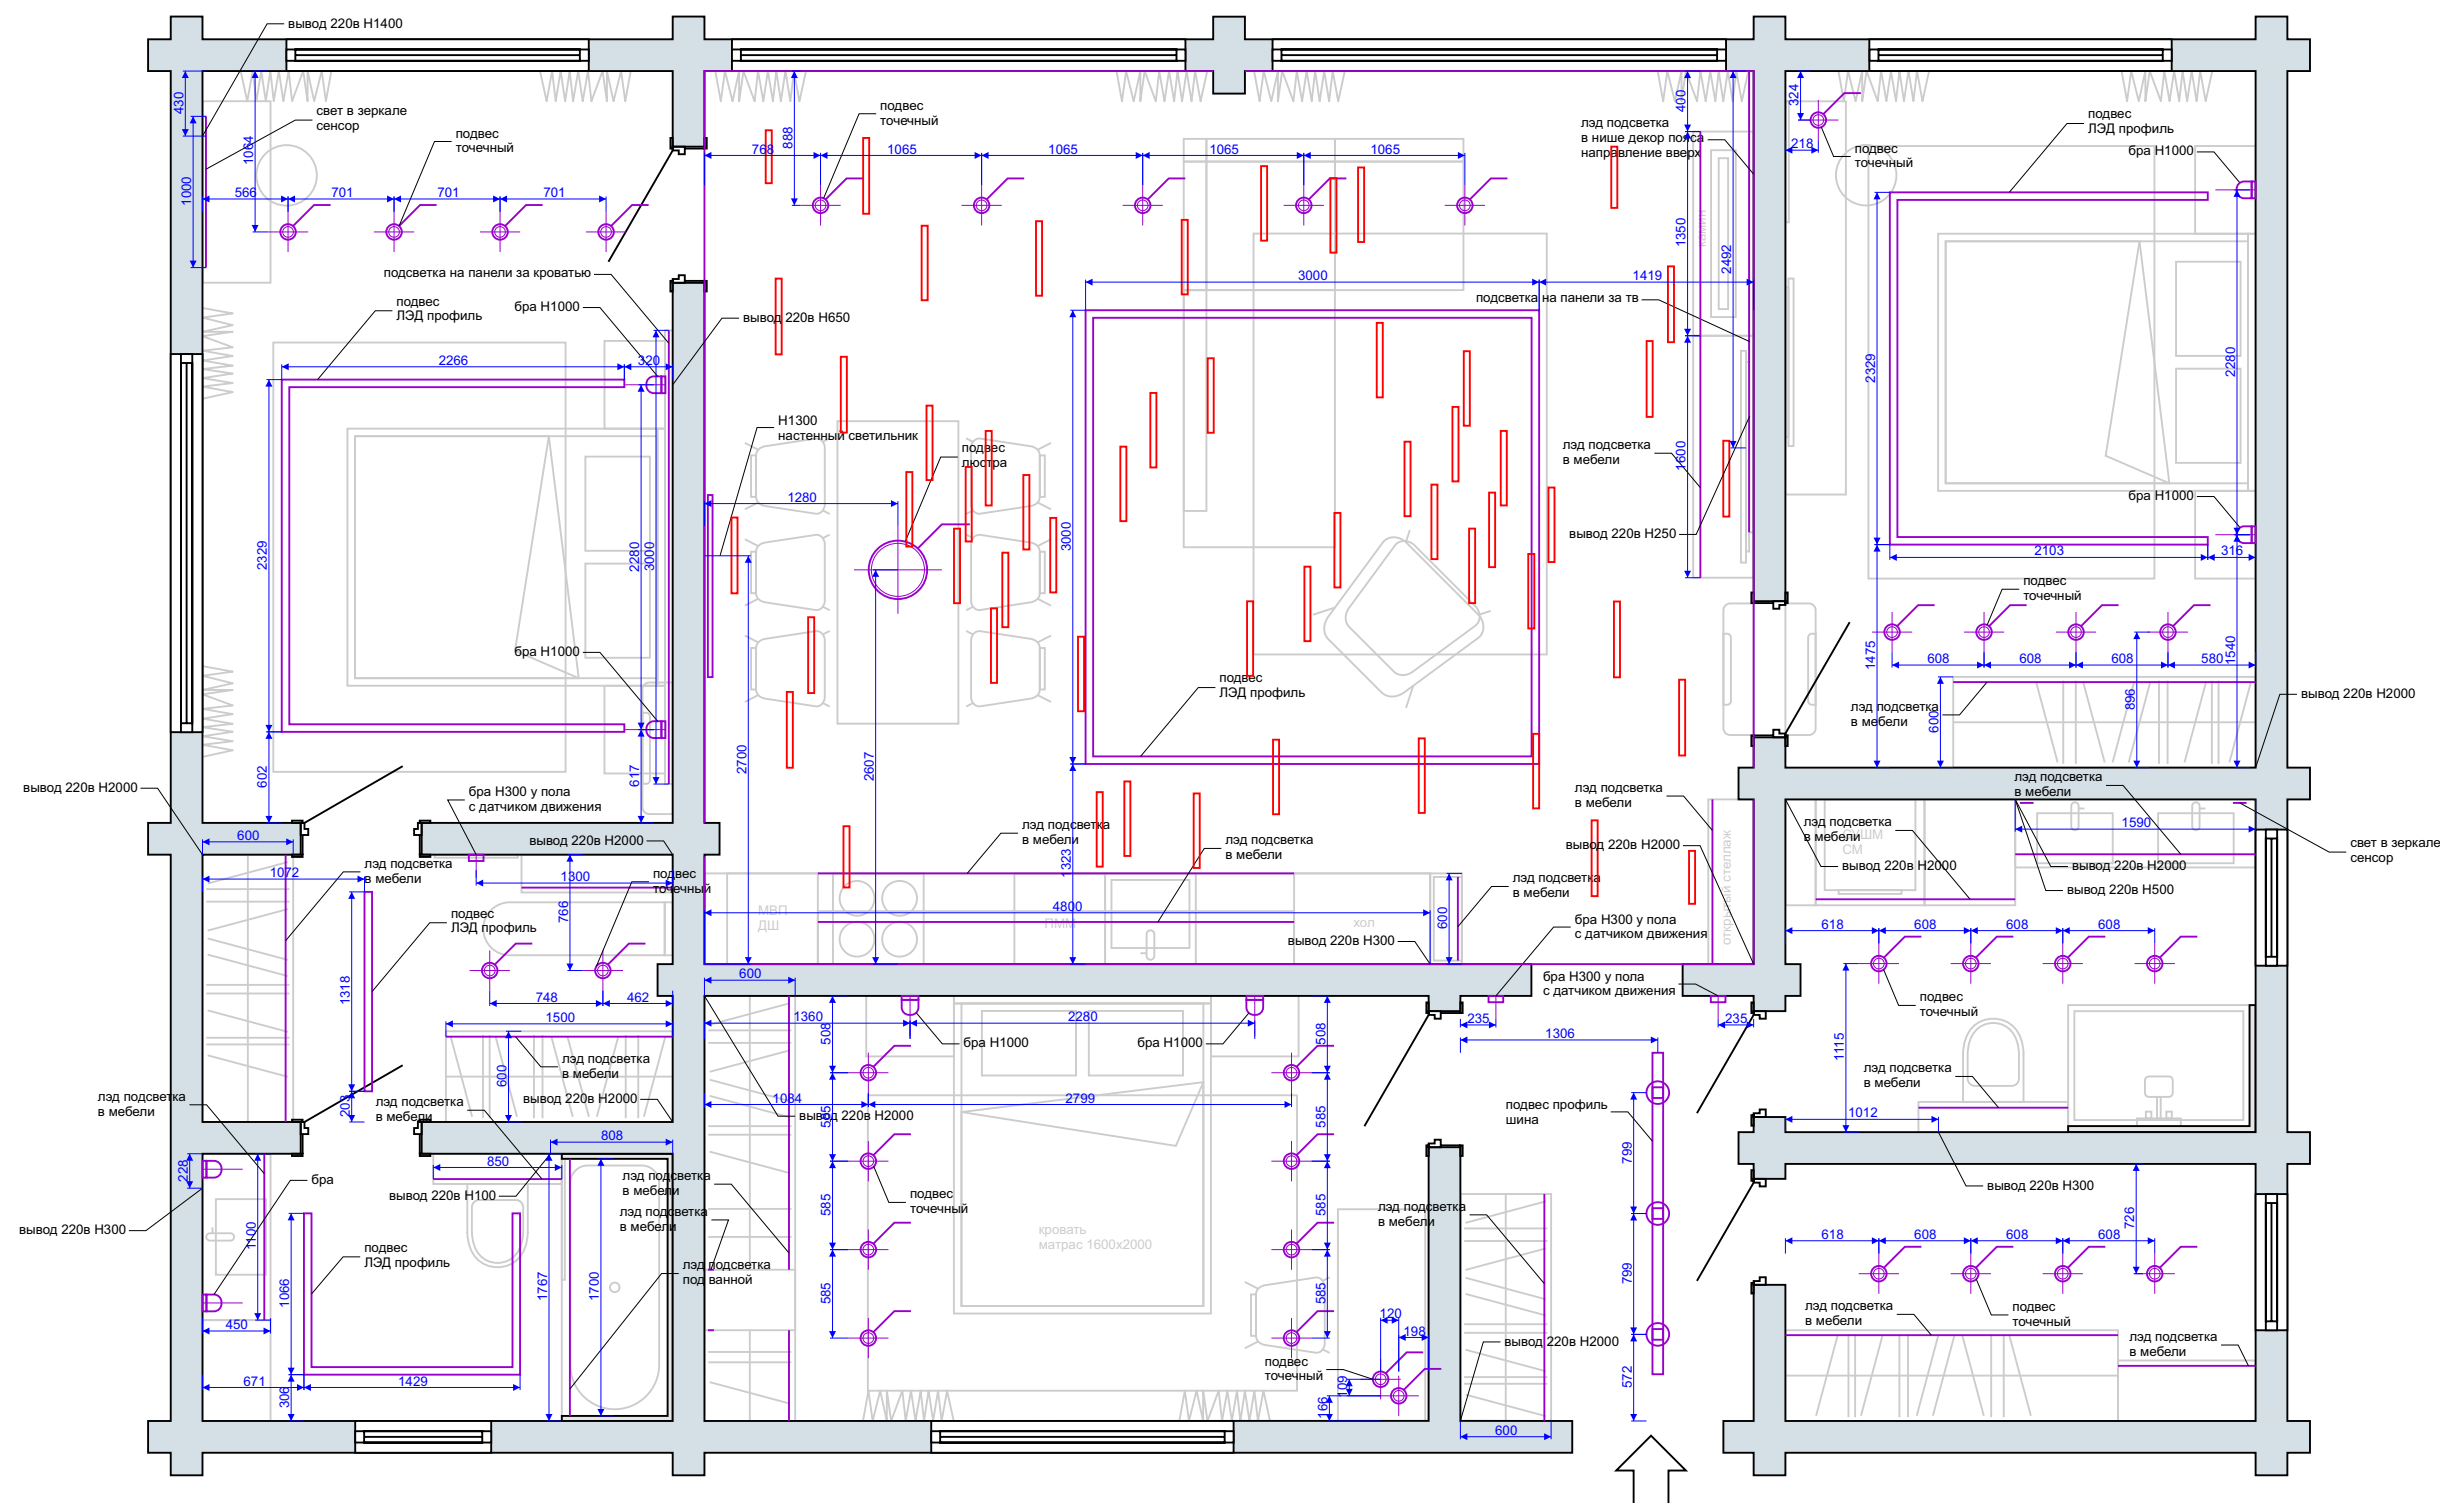

**melnica
_design**


email: melnica1ds@gmail.com
phone: +7 999 466 1896
instagram: @melnica_design

	ФИО	подпись	дата	План светильников		
Выполнил				Жилой дом из бруса		
Согласовал				масштаб 1:50	лист - 10	этаж 1

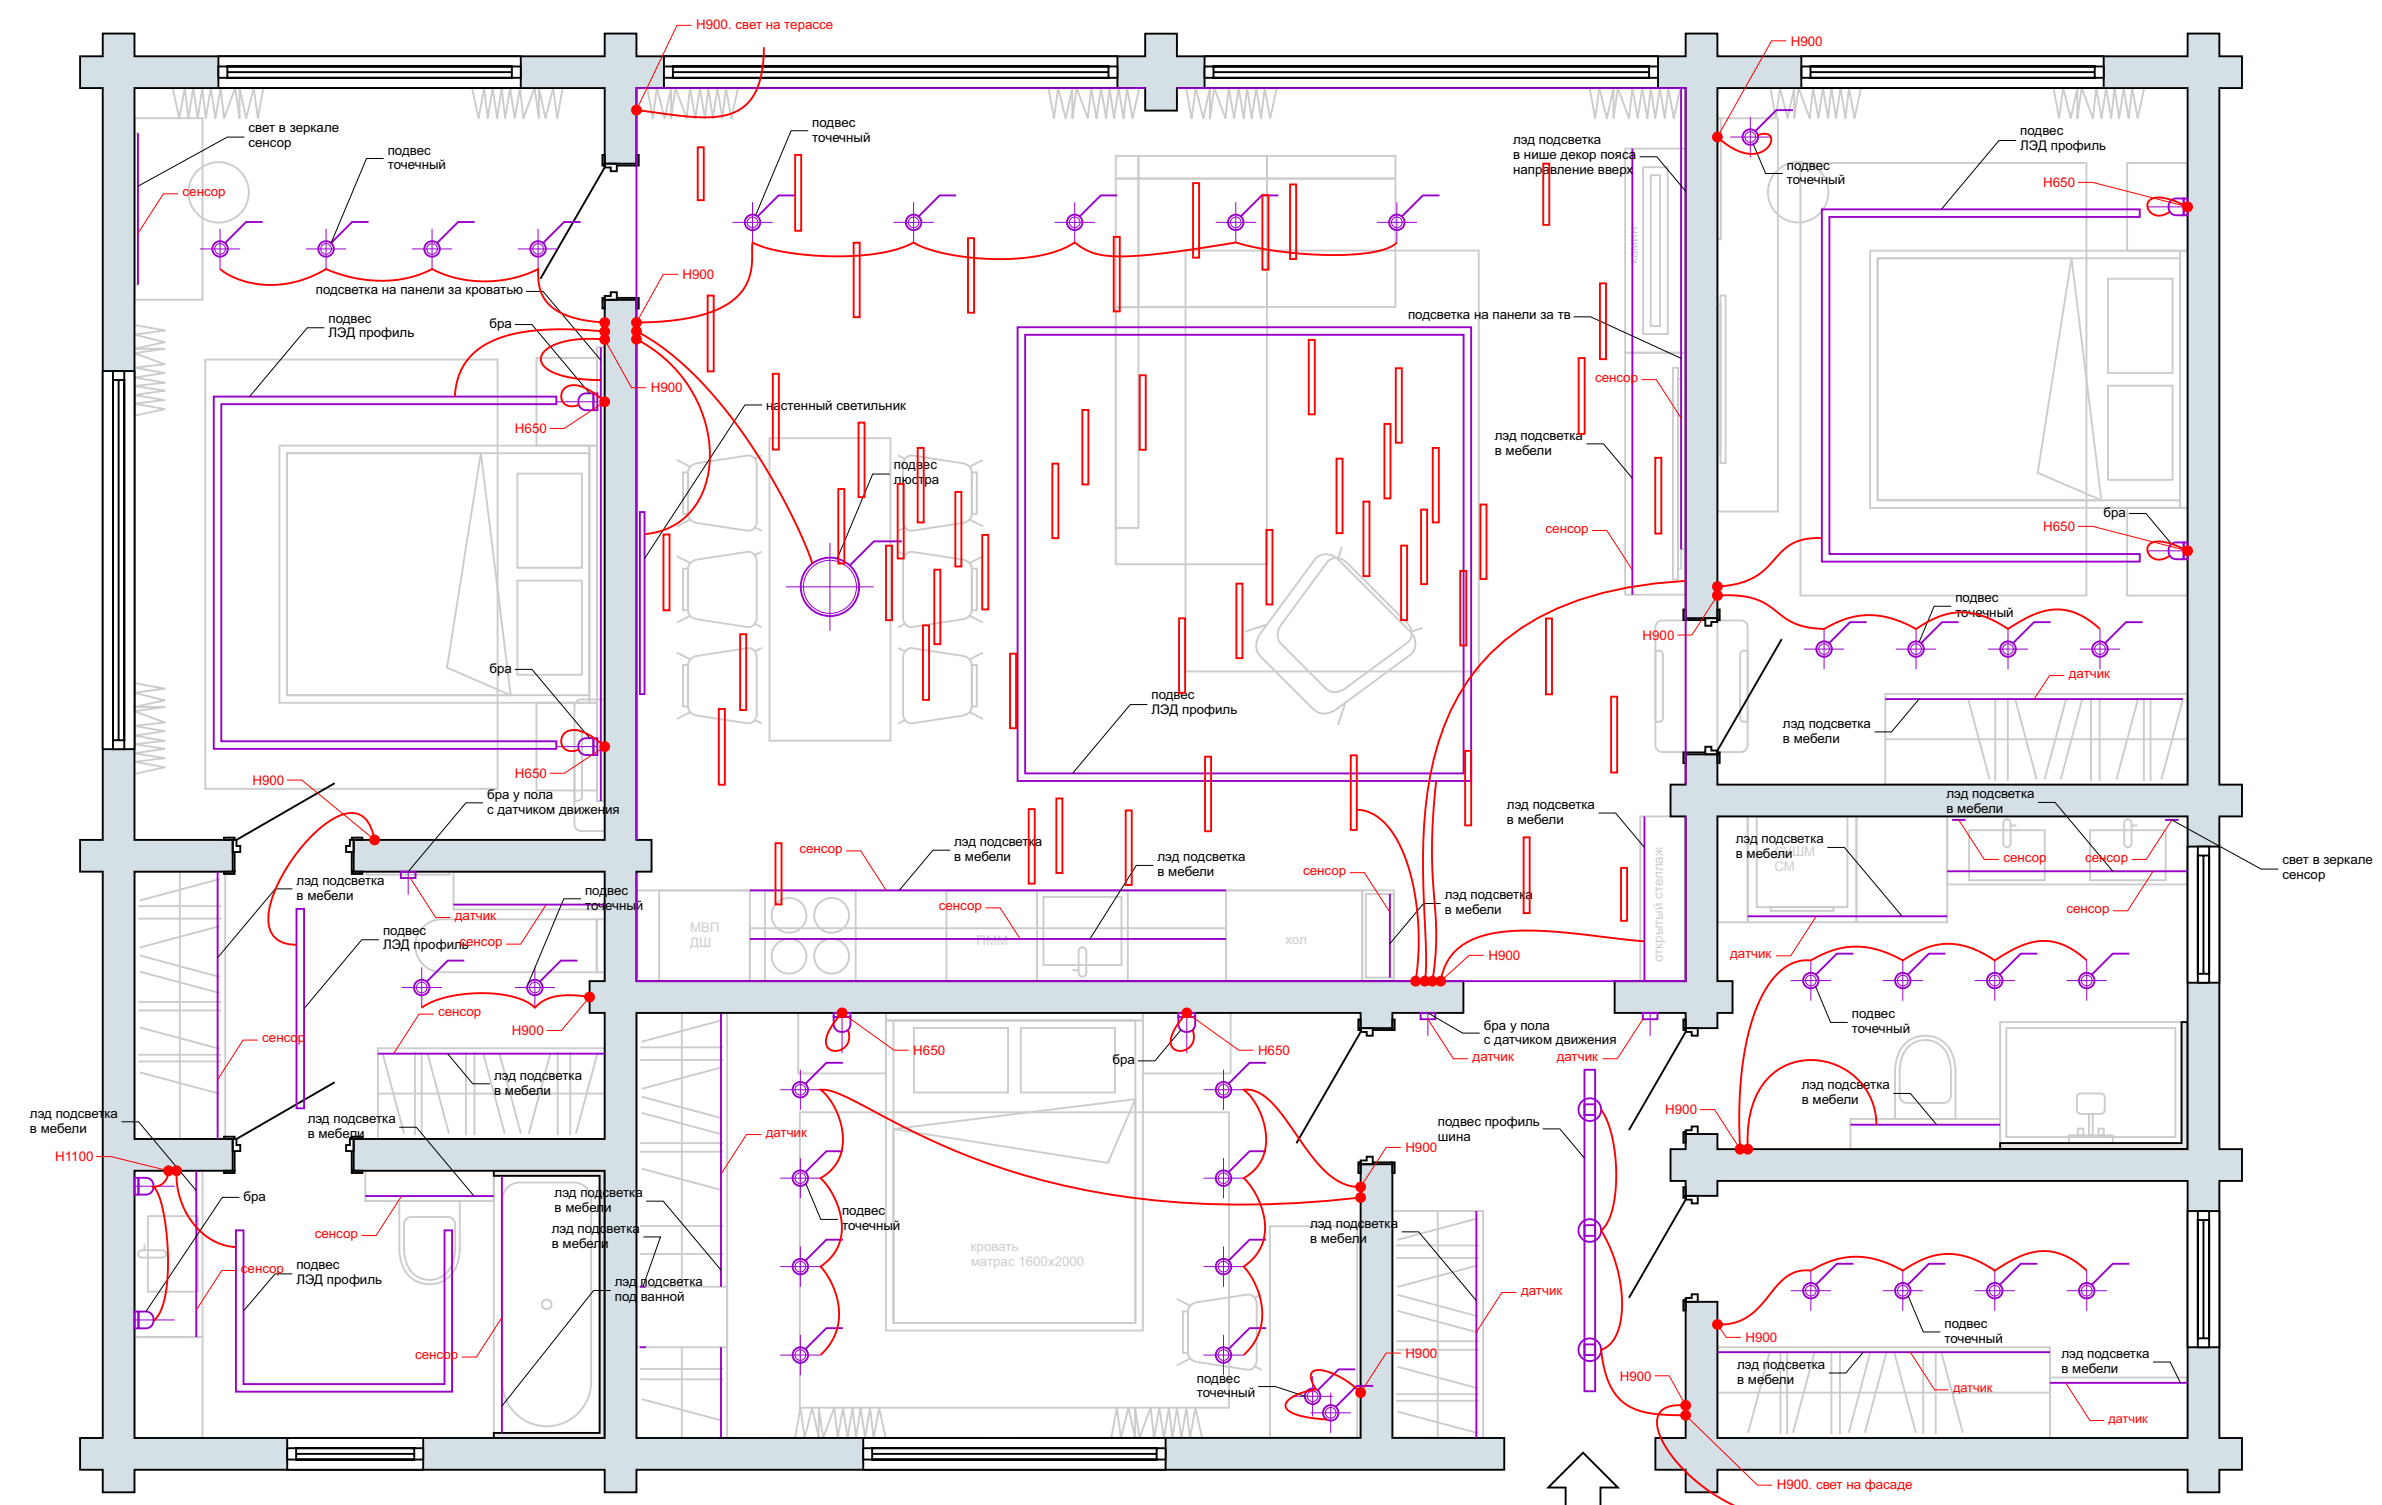

email: melnica1ds@gmail.com
 phone: +7 999 466 1896
 instagram: @melnica_design



	ФИО	подпись	дата	План подключения светильников		
Выполнил				Жилой дом из бруса		
Согласовал				масштаб 1:50	лист - 11	этаж 1

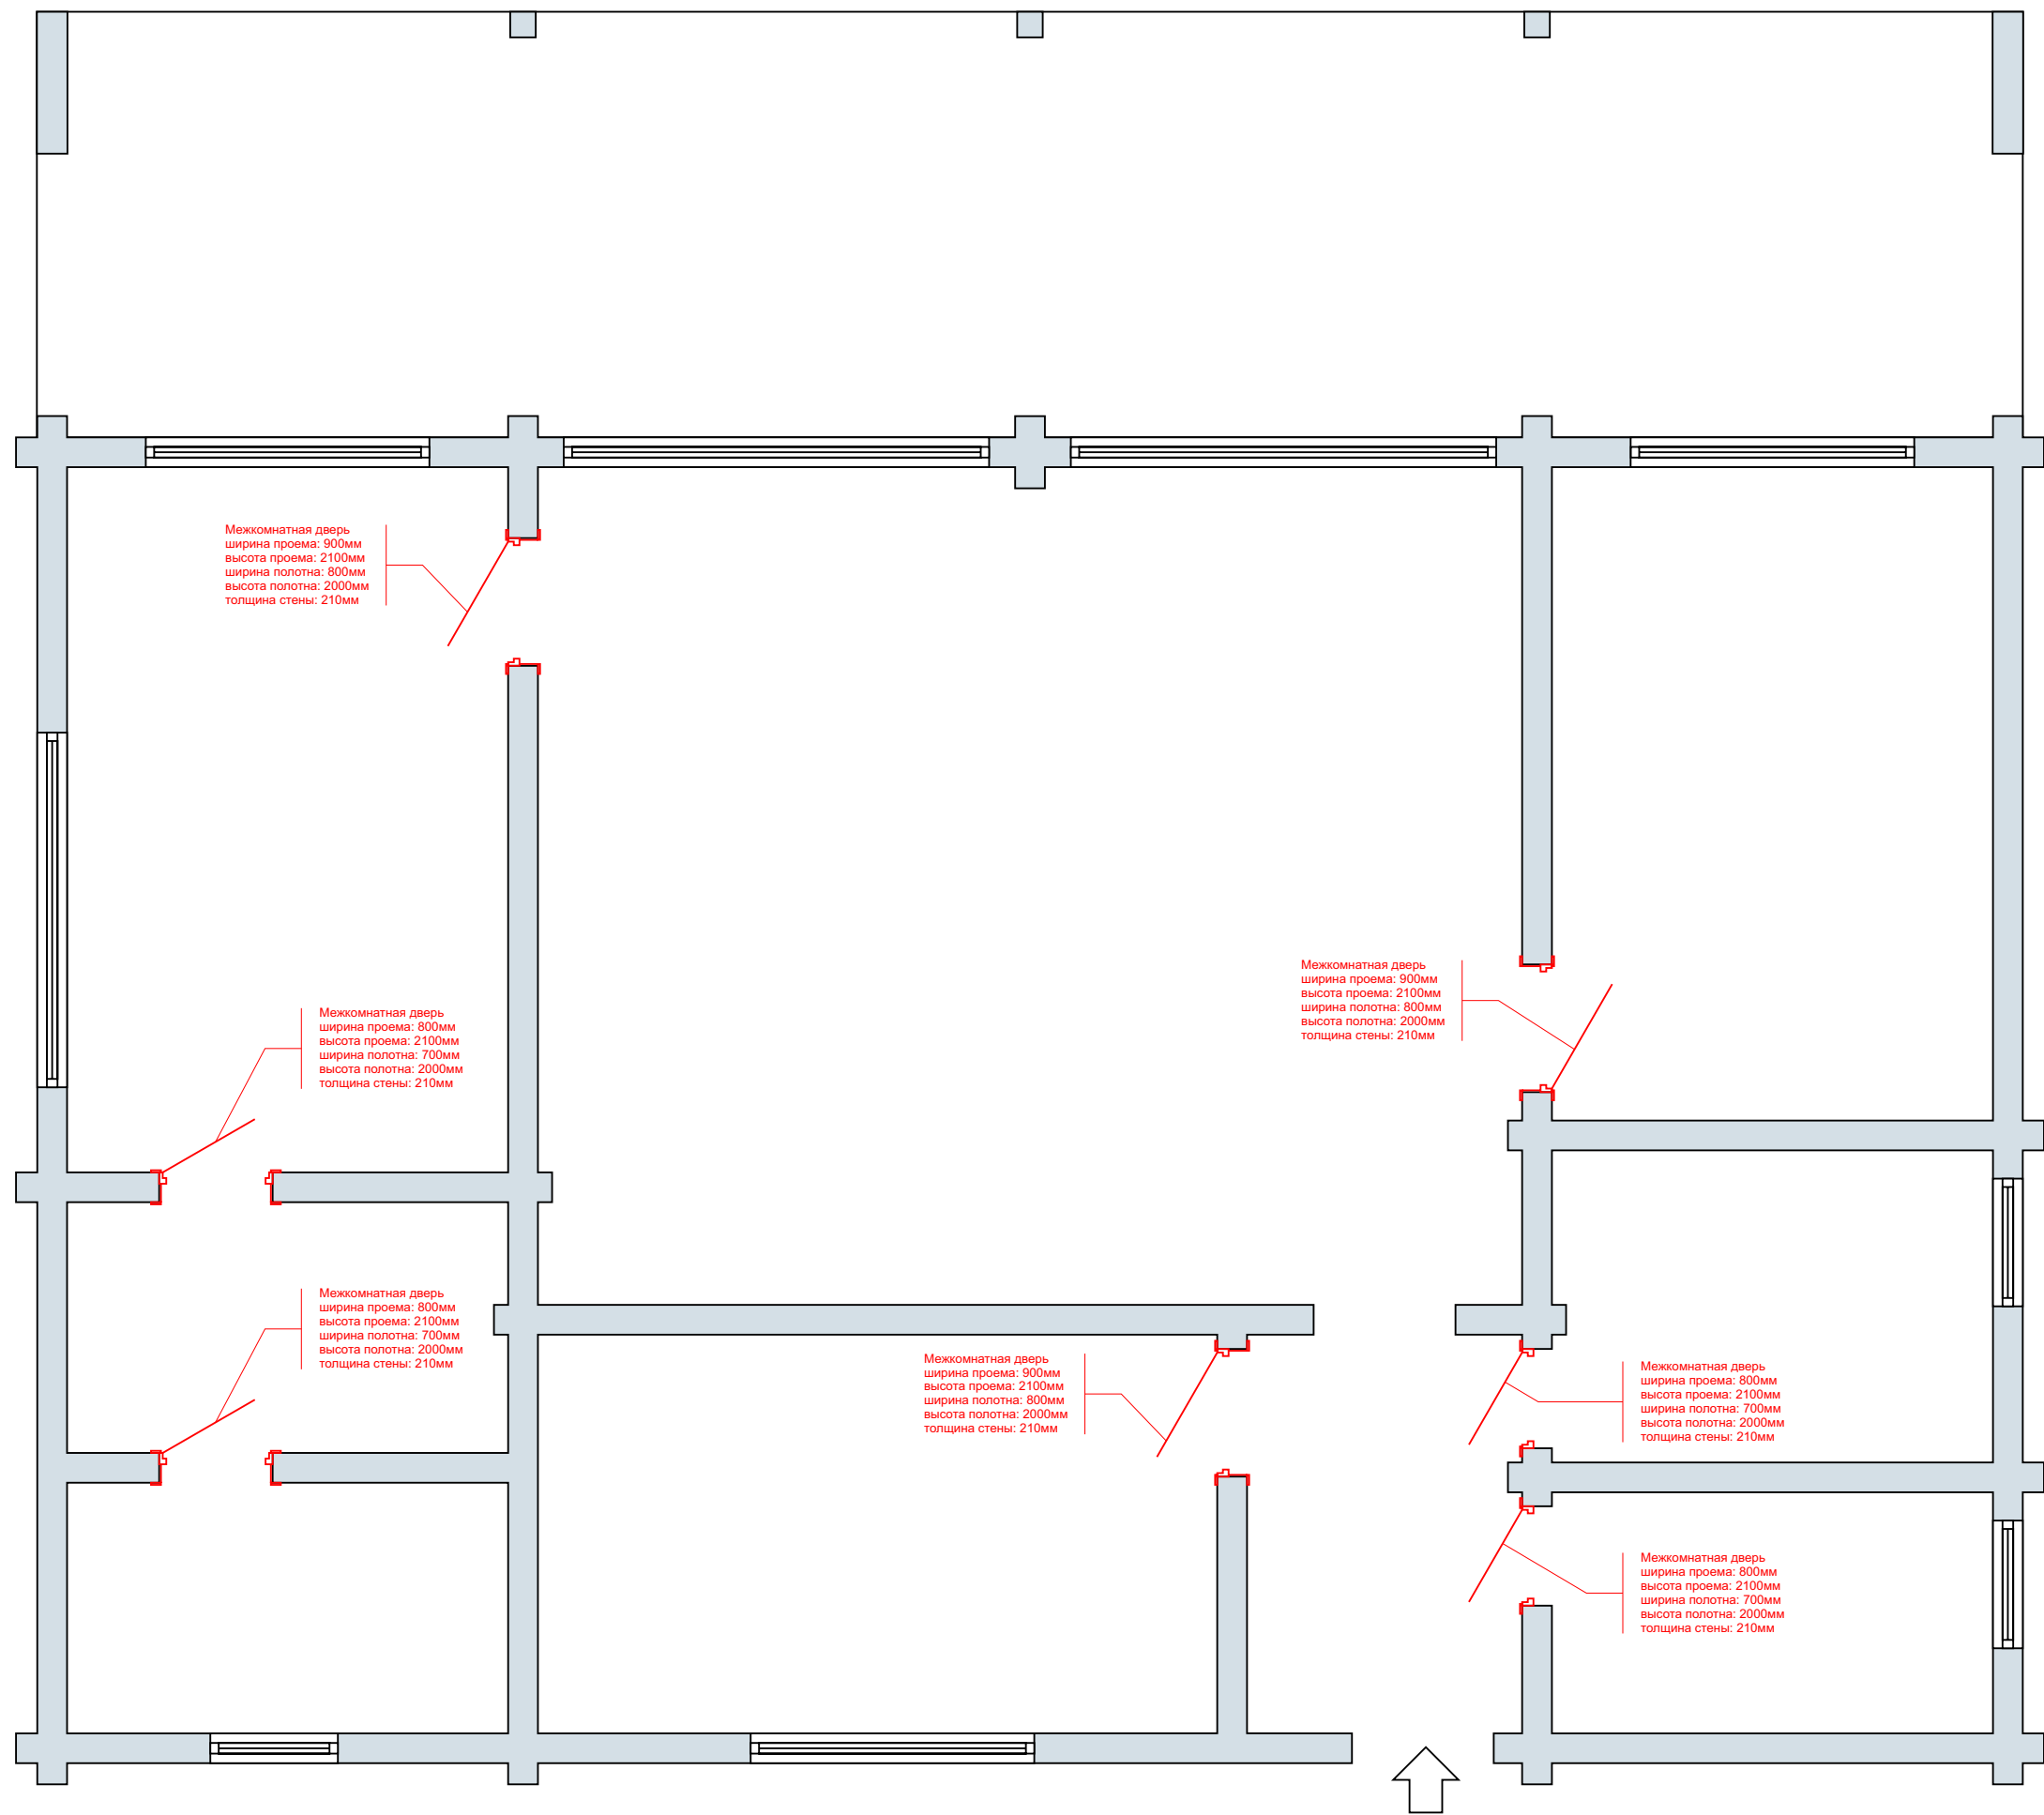

**melnica
_design**

email: melnica1ds@gmail.com
phone: +7 999 466 1896
instagram: @melnica_design



	ФИО	подпись	дата	План дверей		
Выполнил				Жилой дом из бруса		
Согласовал				масштаб 1:50	лист - 13	этаж 1

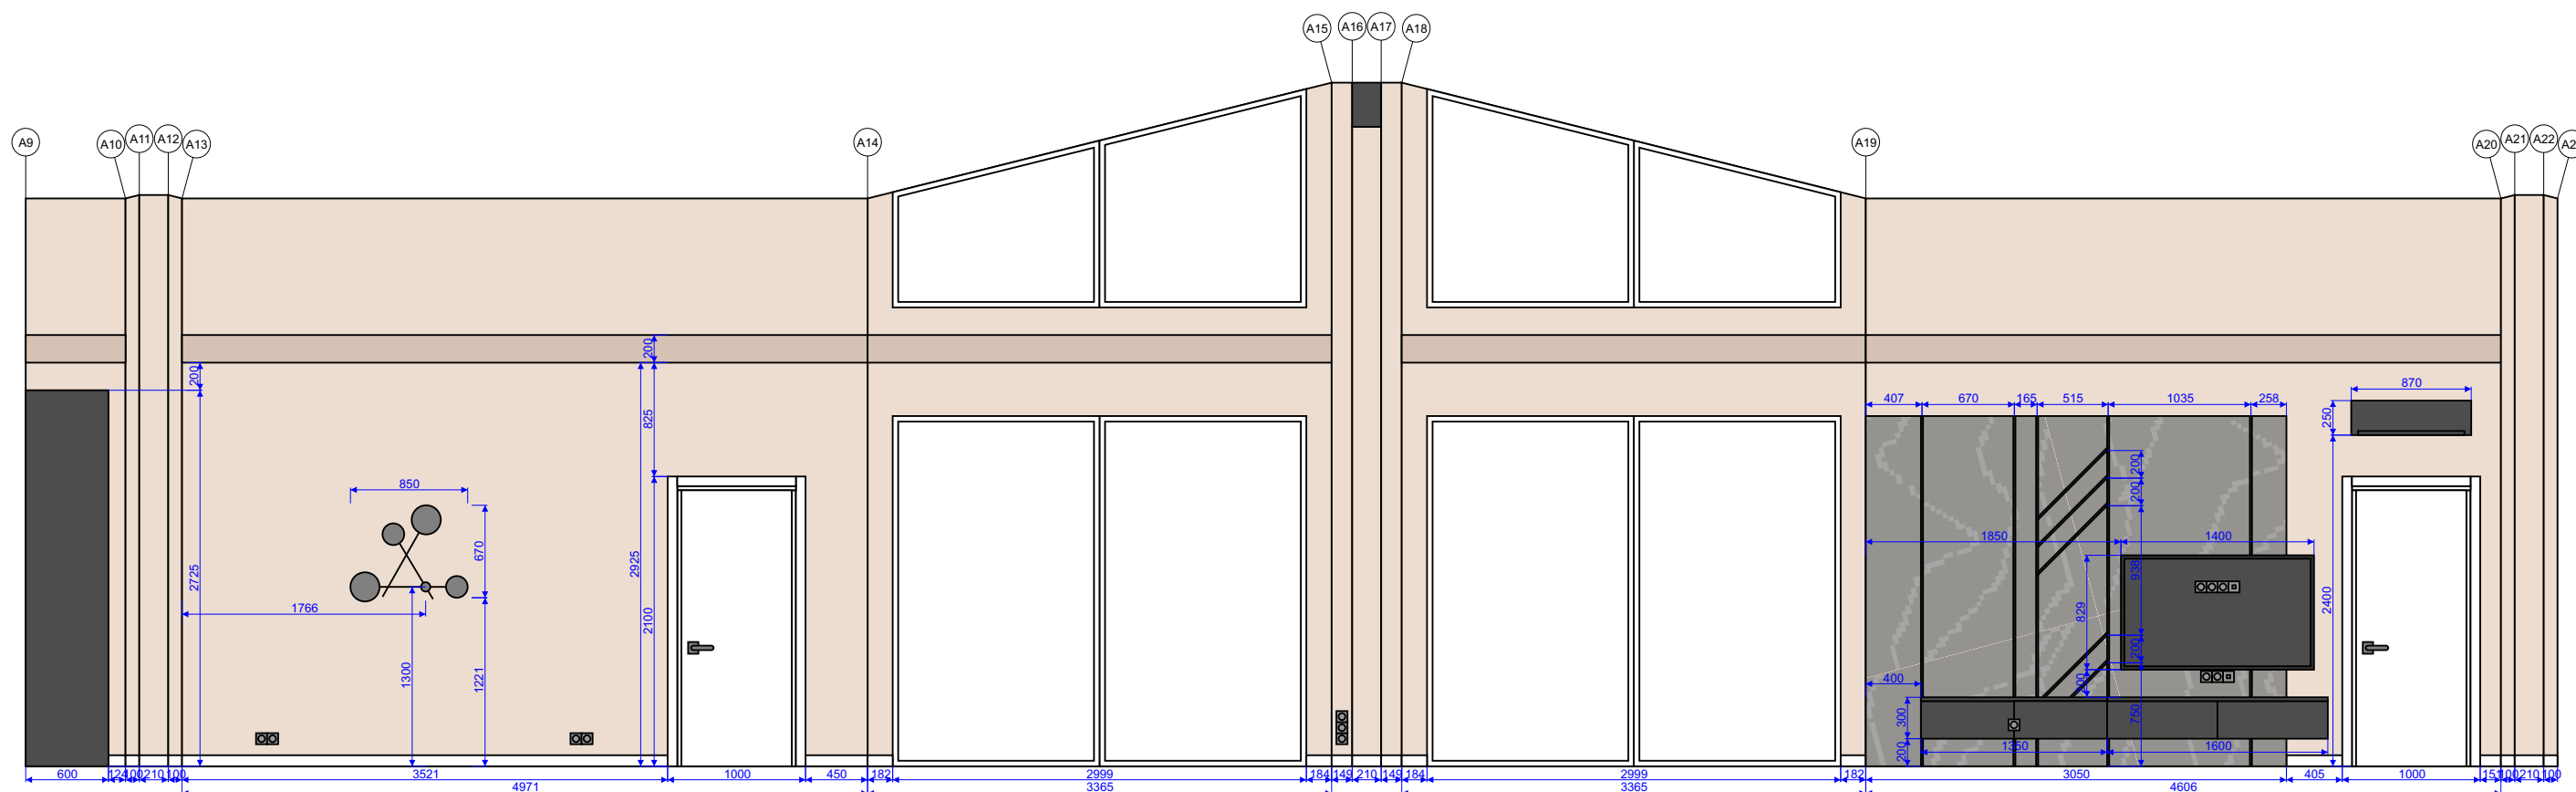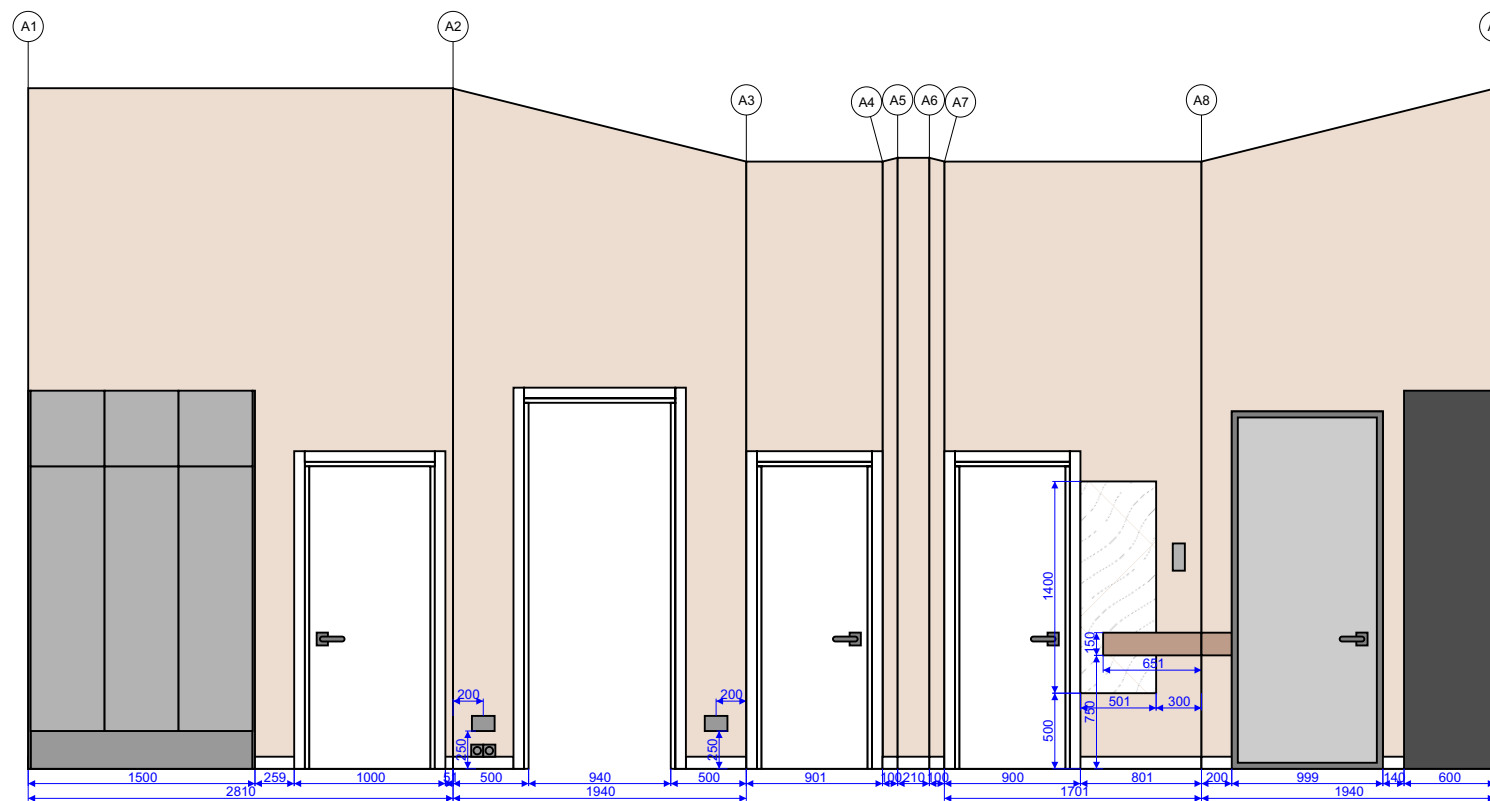

**melnica
_design**



email: melnica1ds@gmail.com
phone: +7 999 466 1896
instagram: @melnica_design

	ФИО	подпись	дата	Развертка стен		
Выполнил				Жилой дом из бруса		
Согласовал				масштаб 1:50	лист - 15	этаж 1

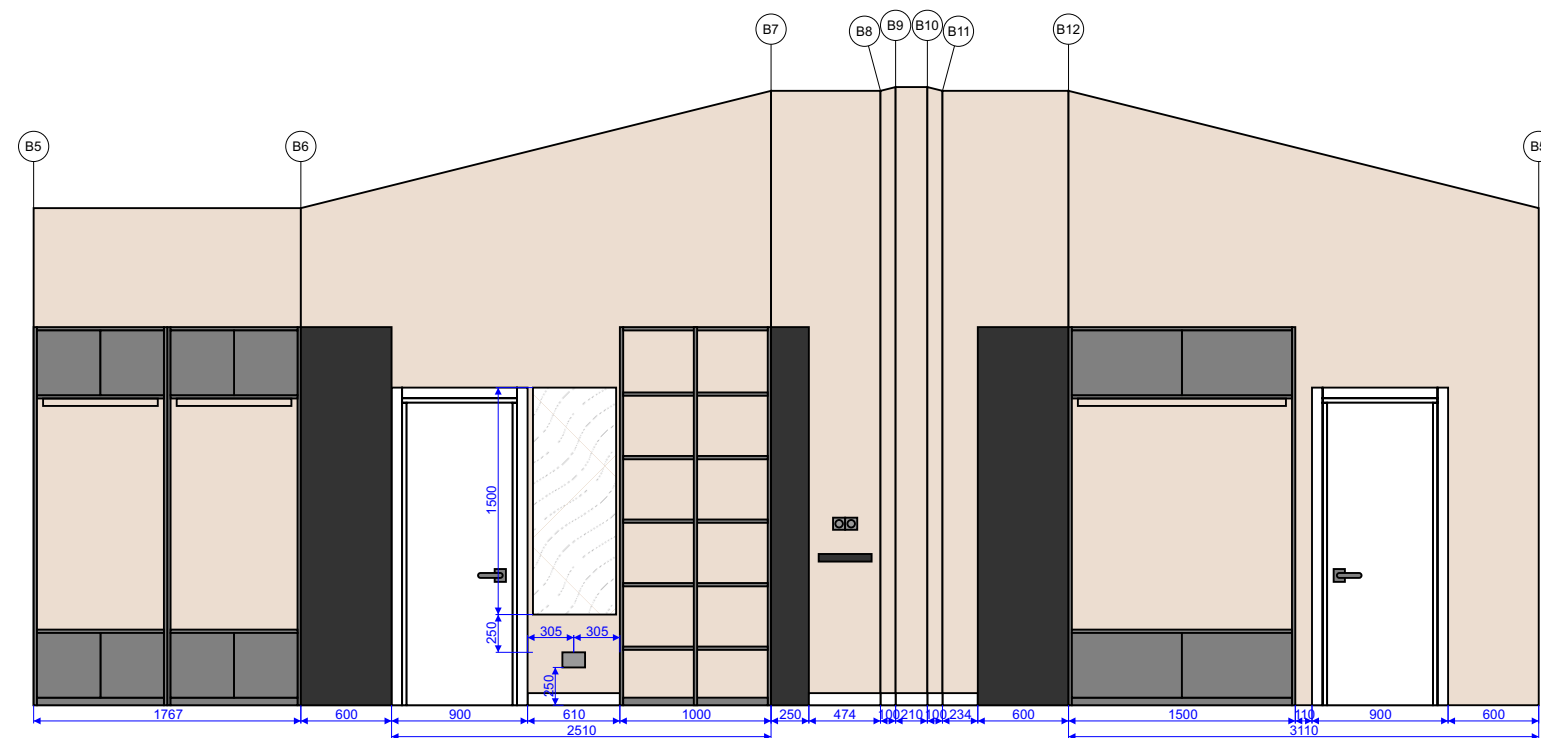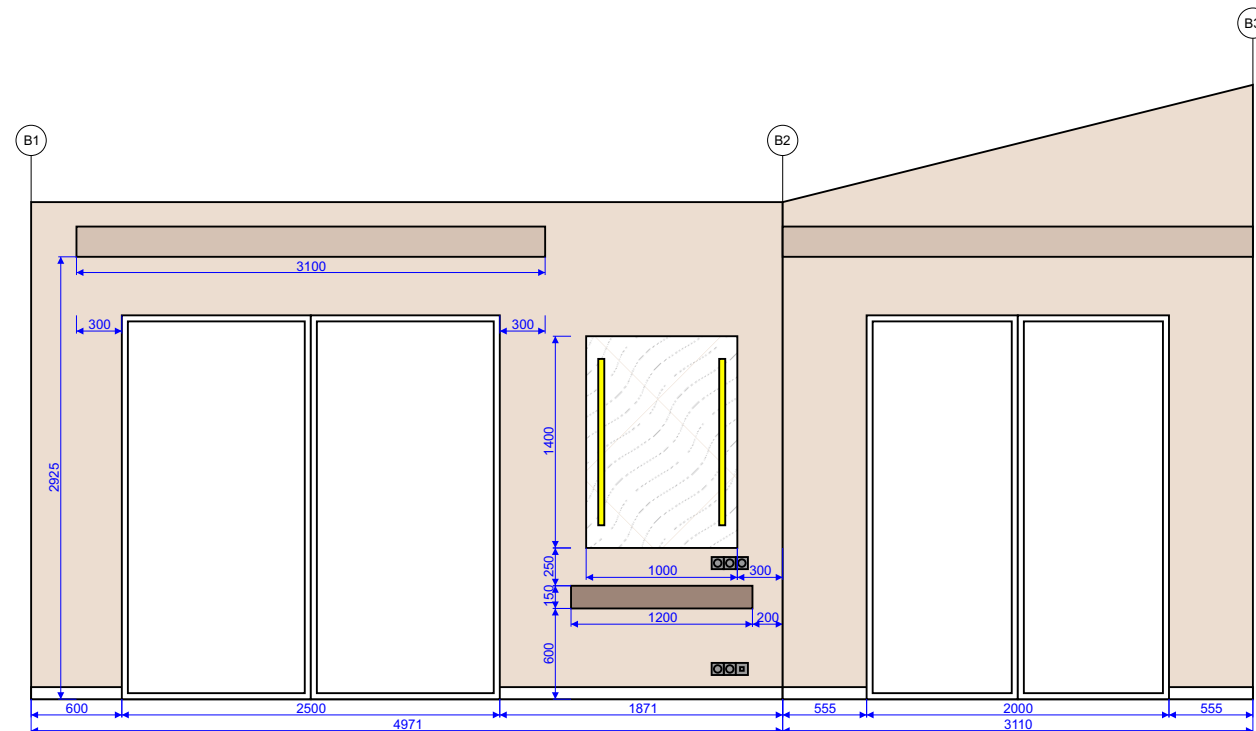

email: melnica1ds@gmail.com
phone: +7 999 466 1896
instagram: @melnica_design


	ФИО	подпись	дата	Развертка стен		
Выполнил				Жилой дом из бруса		
Согласовал				масштаб 1:50	лист - 16	этаж 1

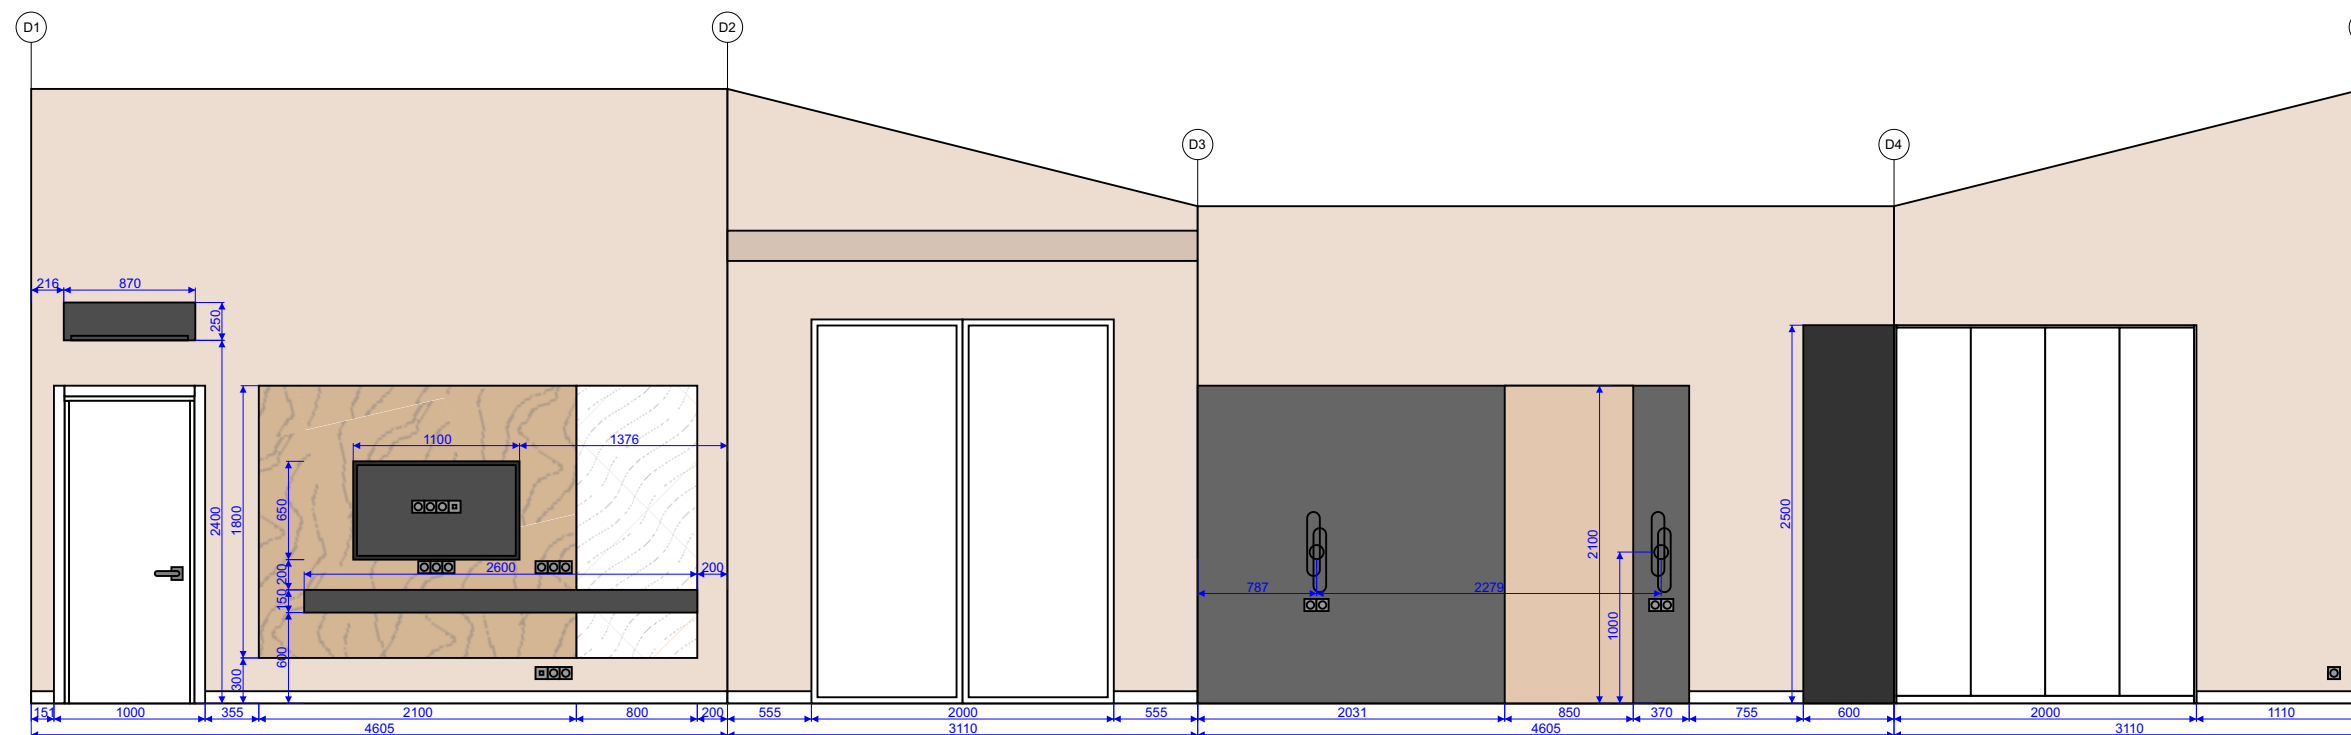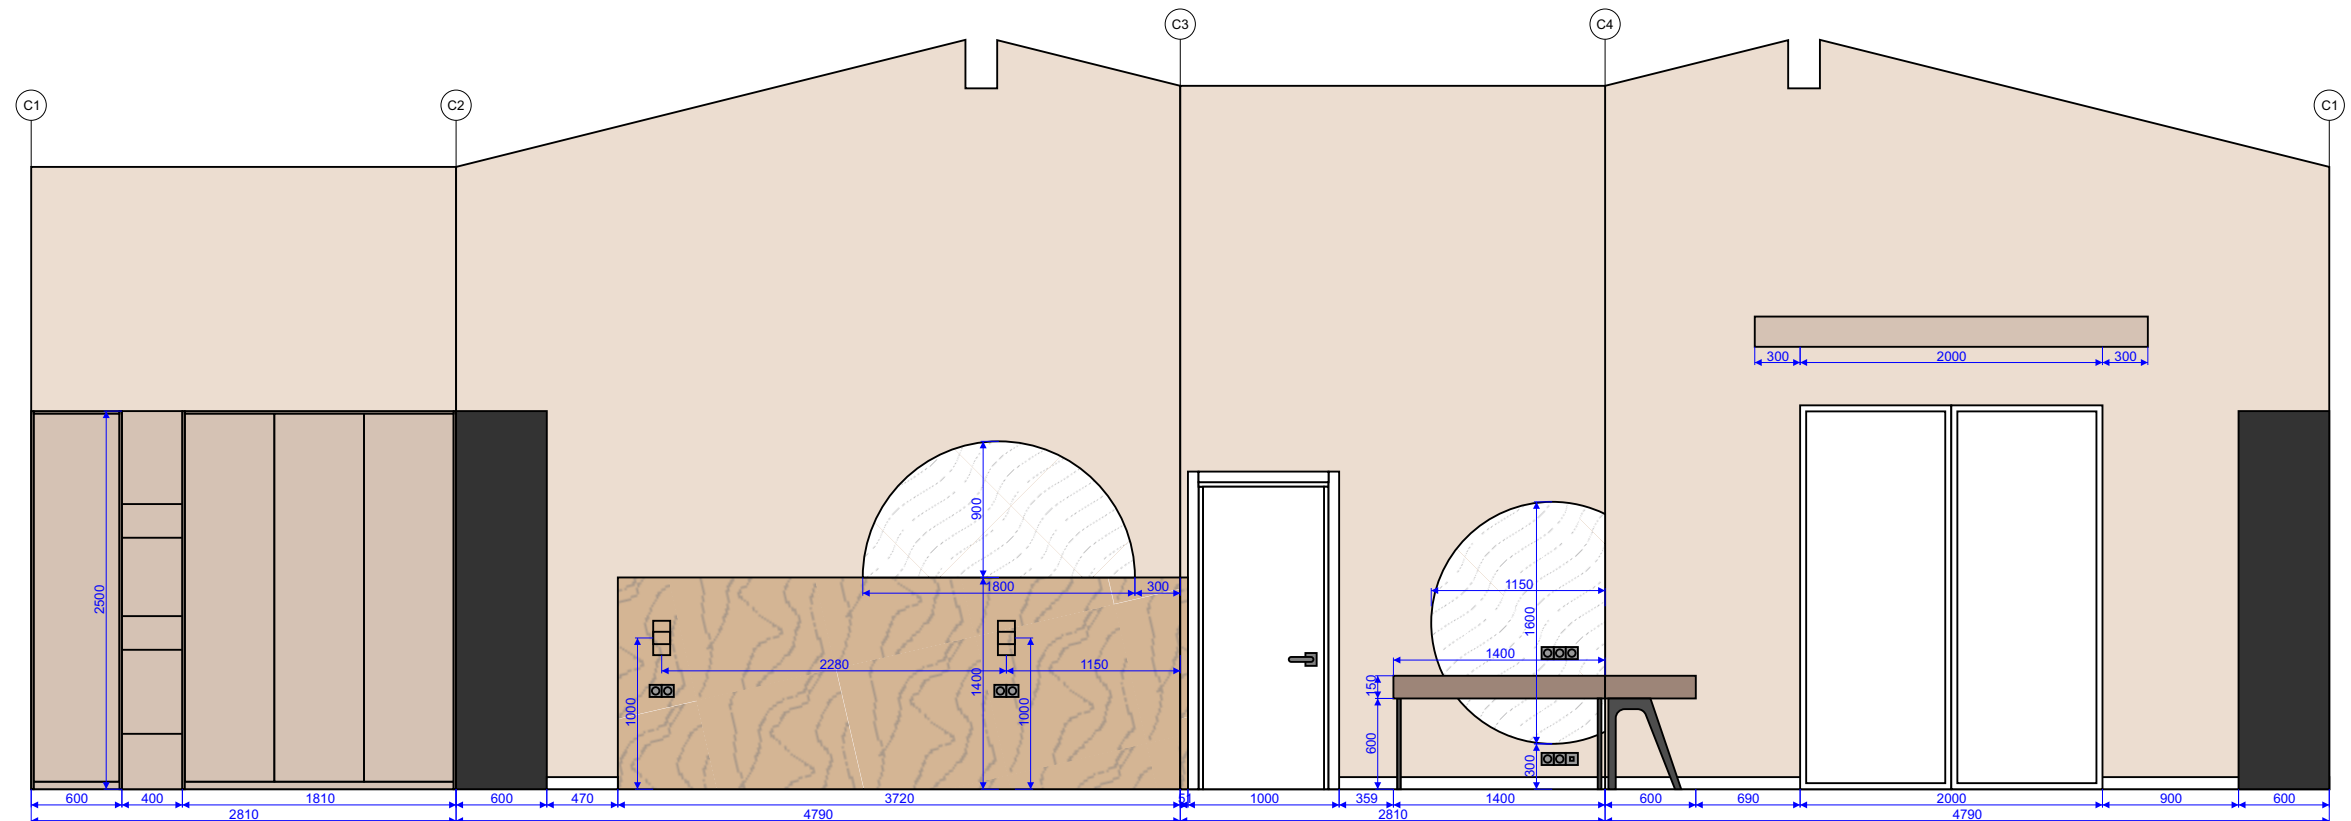

**melnica
_design**

email: melnica1ds@gmail.com
phone: +7 999 466 1896
instagram: @melnica_design





	ФИО	подпись	дата	Развертка стен		
Выполнил				Жилой дом из бруса		
Согласовал				масштаб 1:50	лист - 17	этаж 1

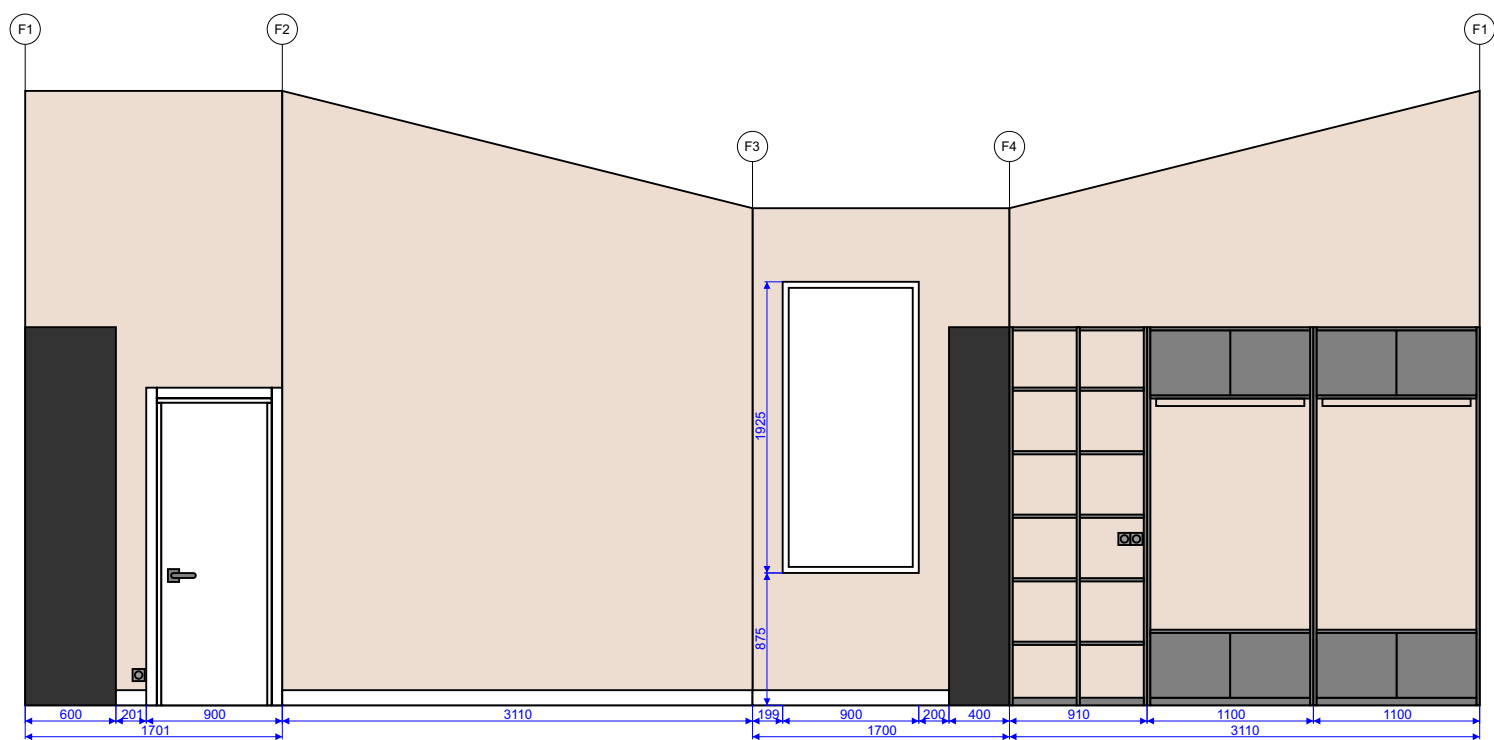

melnica
_design

email: melnica1ds@gmail.com
phone: +7 999 466 1896
instagram: @melnica_design

	ФИО	подпись	дата	Развертка стен		
Выполнил				Жилой дом из бруса		
Согласовал				масштаб 1:50	лист - 18	этаж 1

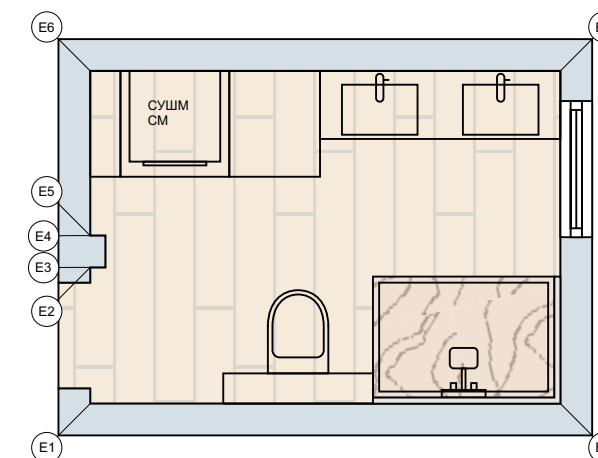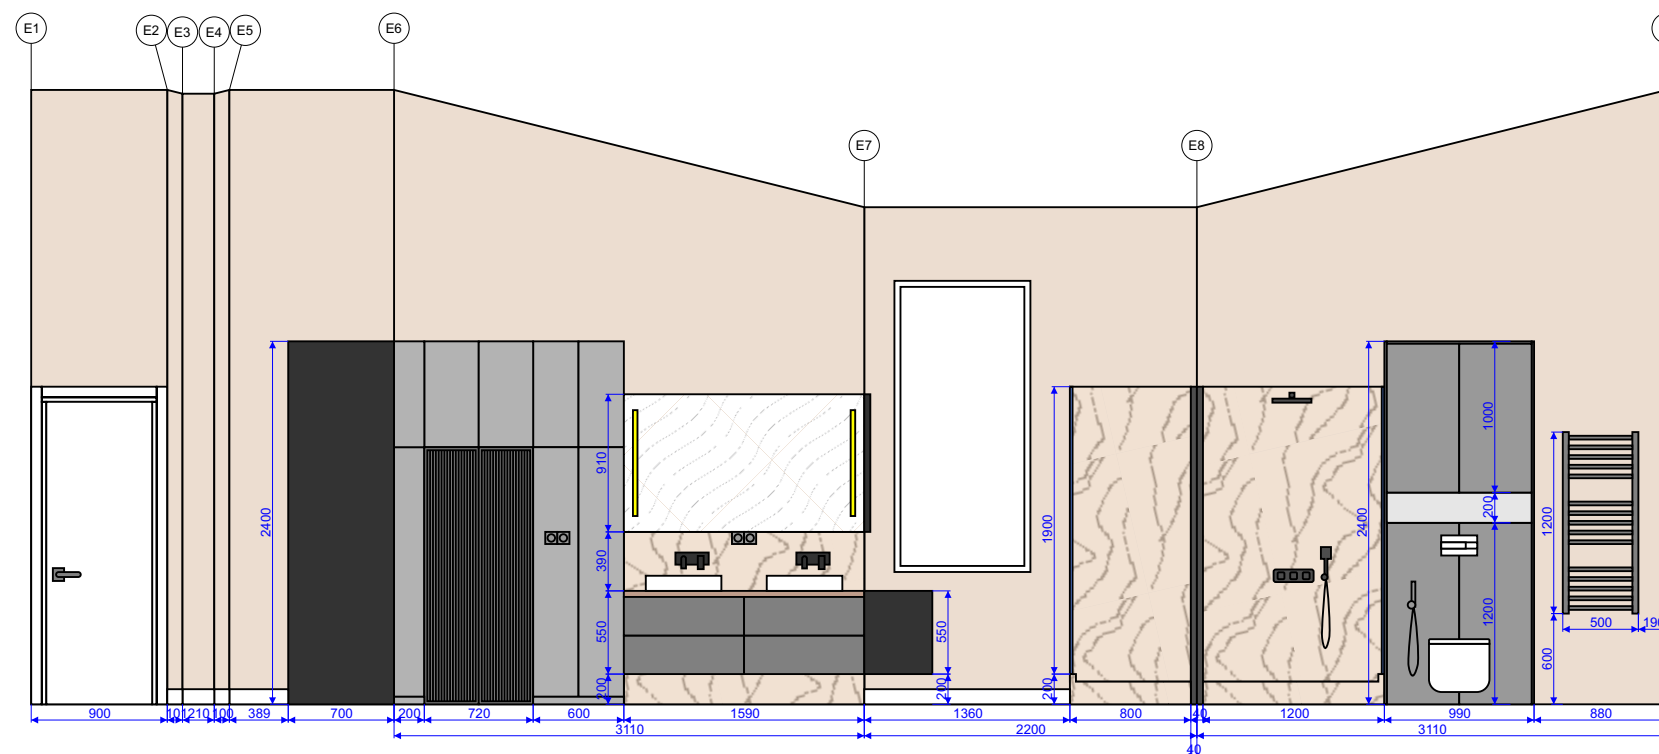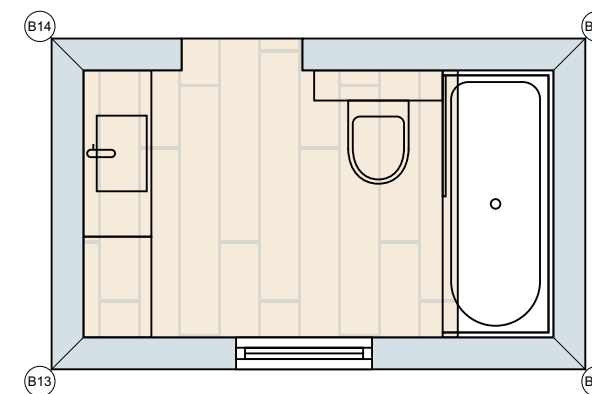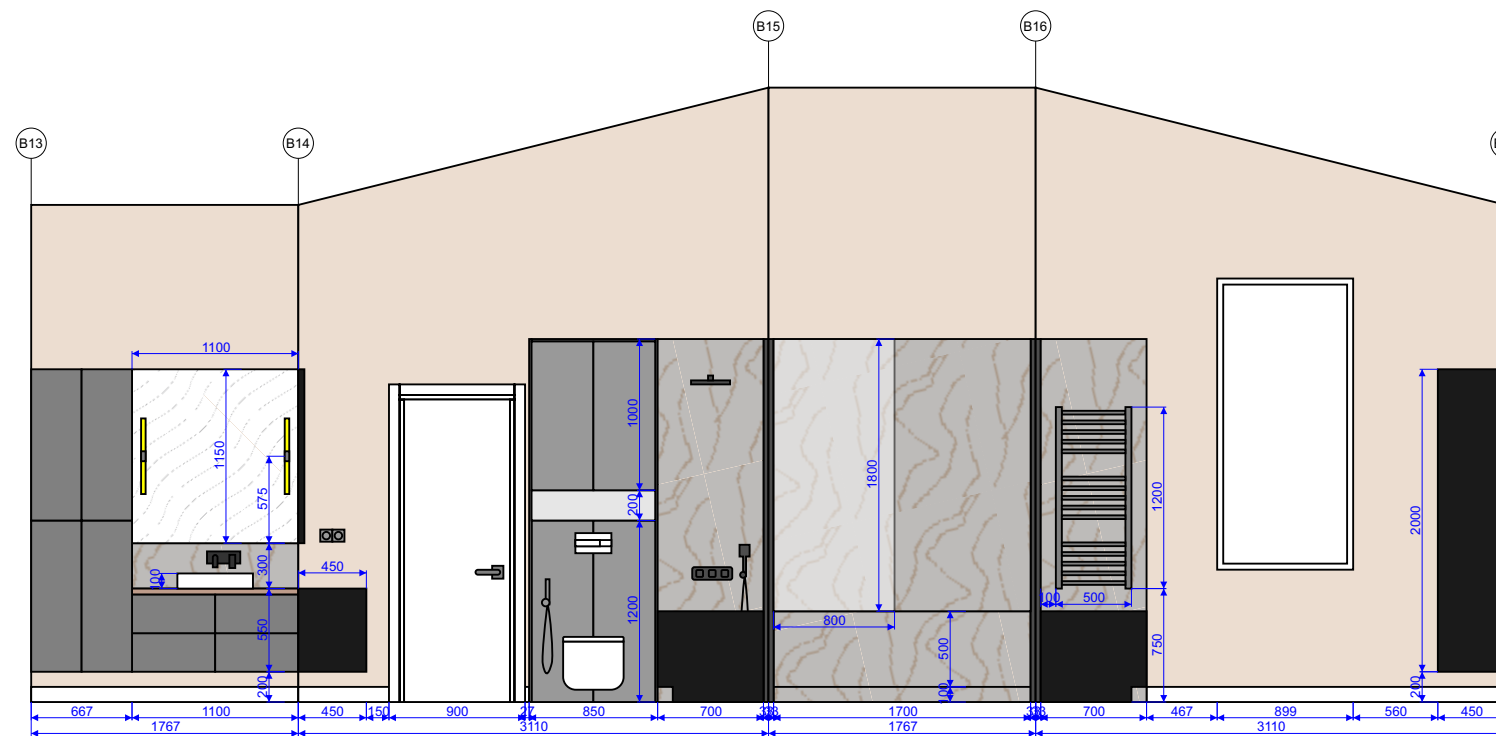

**melnica
_design**

email: melnica1ds@gmail.com
phone: +7 999 466 1896
instagram: @melnica_design

	ФИО	подпись	дата	Развертка стен		
Выполнил				Жилой дом из бруса		
Согласовал				масштаб 1:50	лист - 19	этаж 1